



Indoor Pod

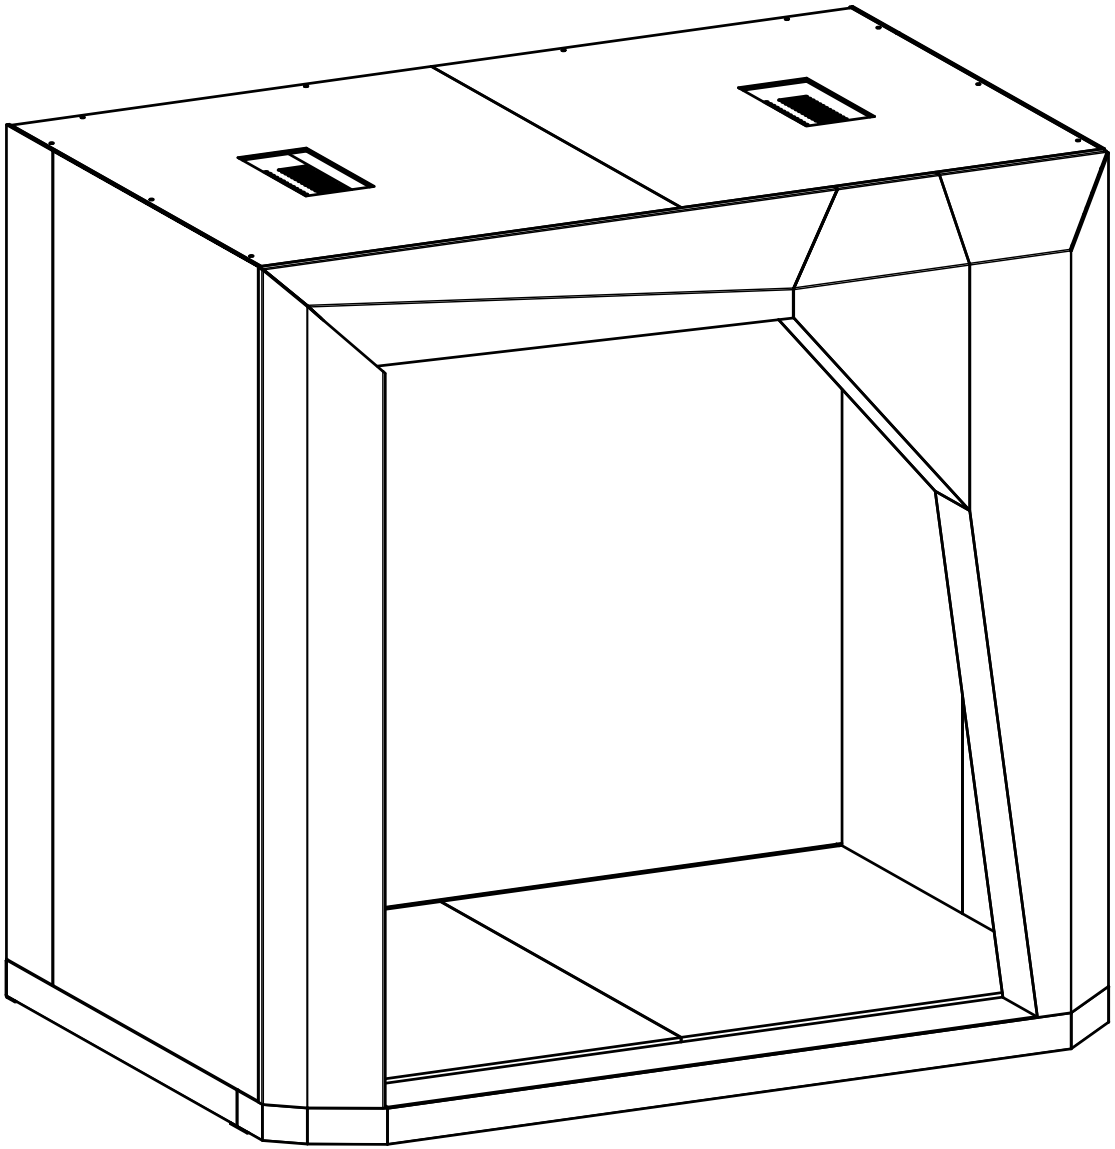

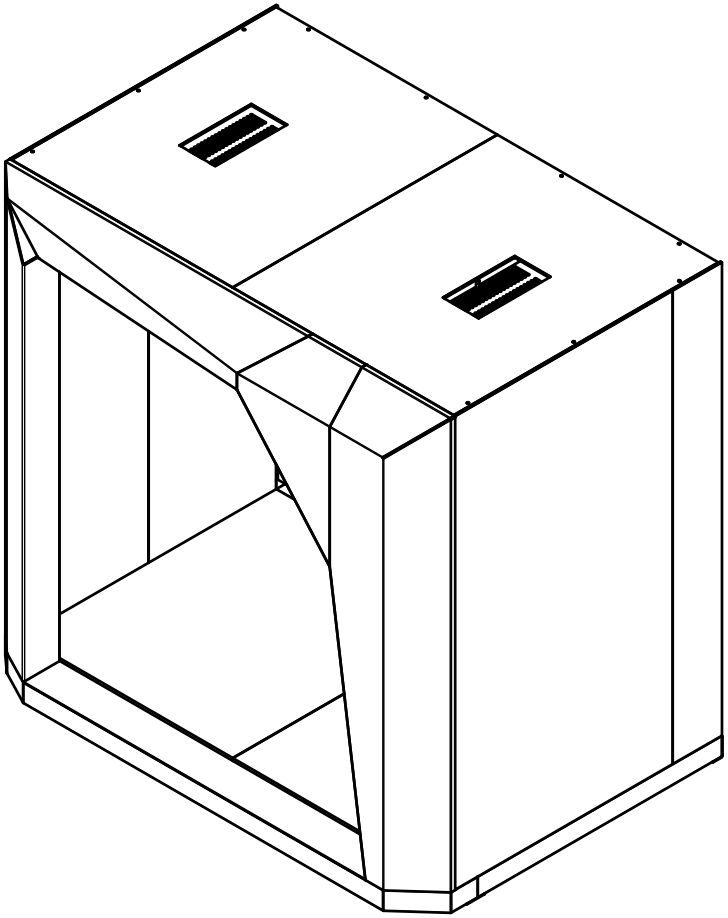


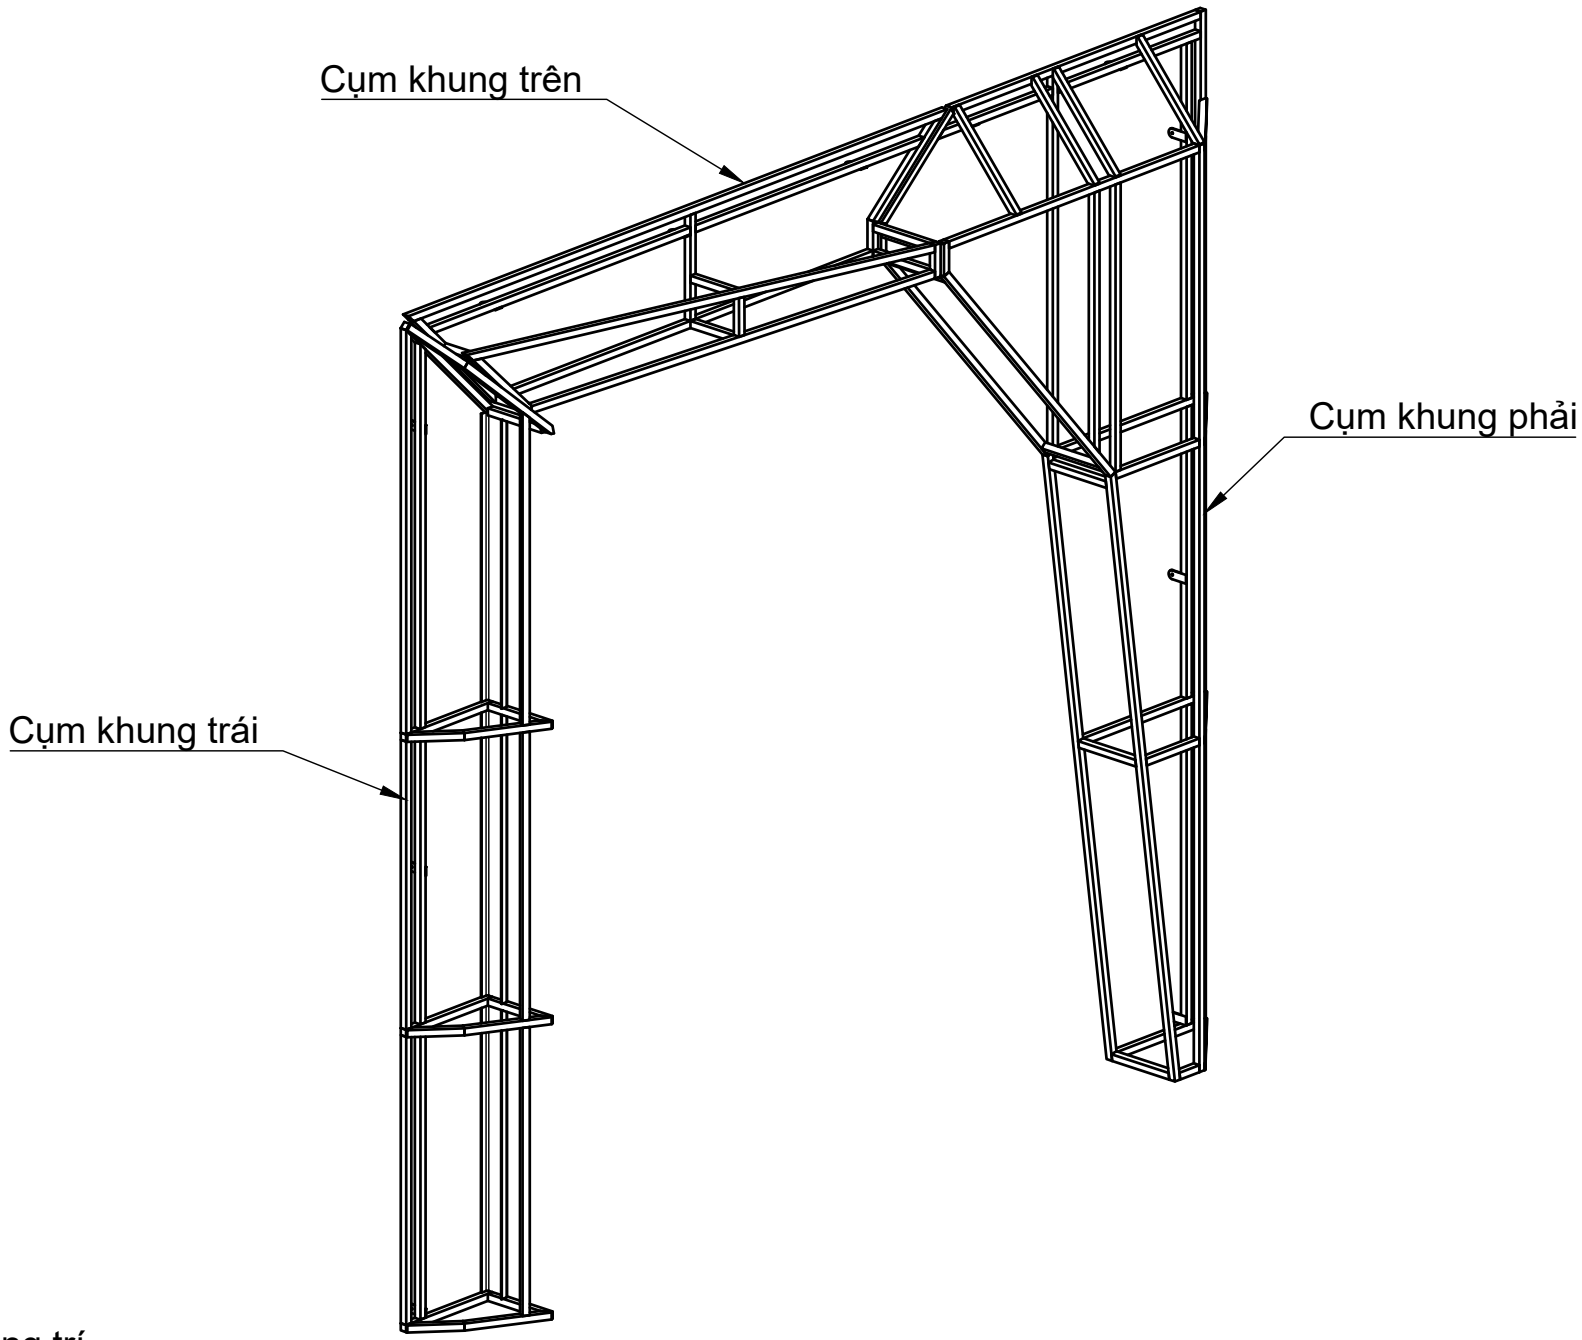



Cụm khung trang trí
SL: 01

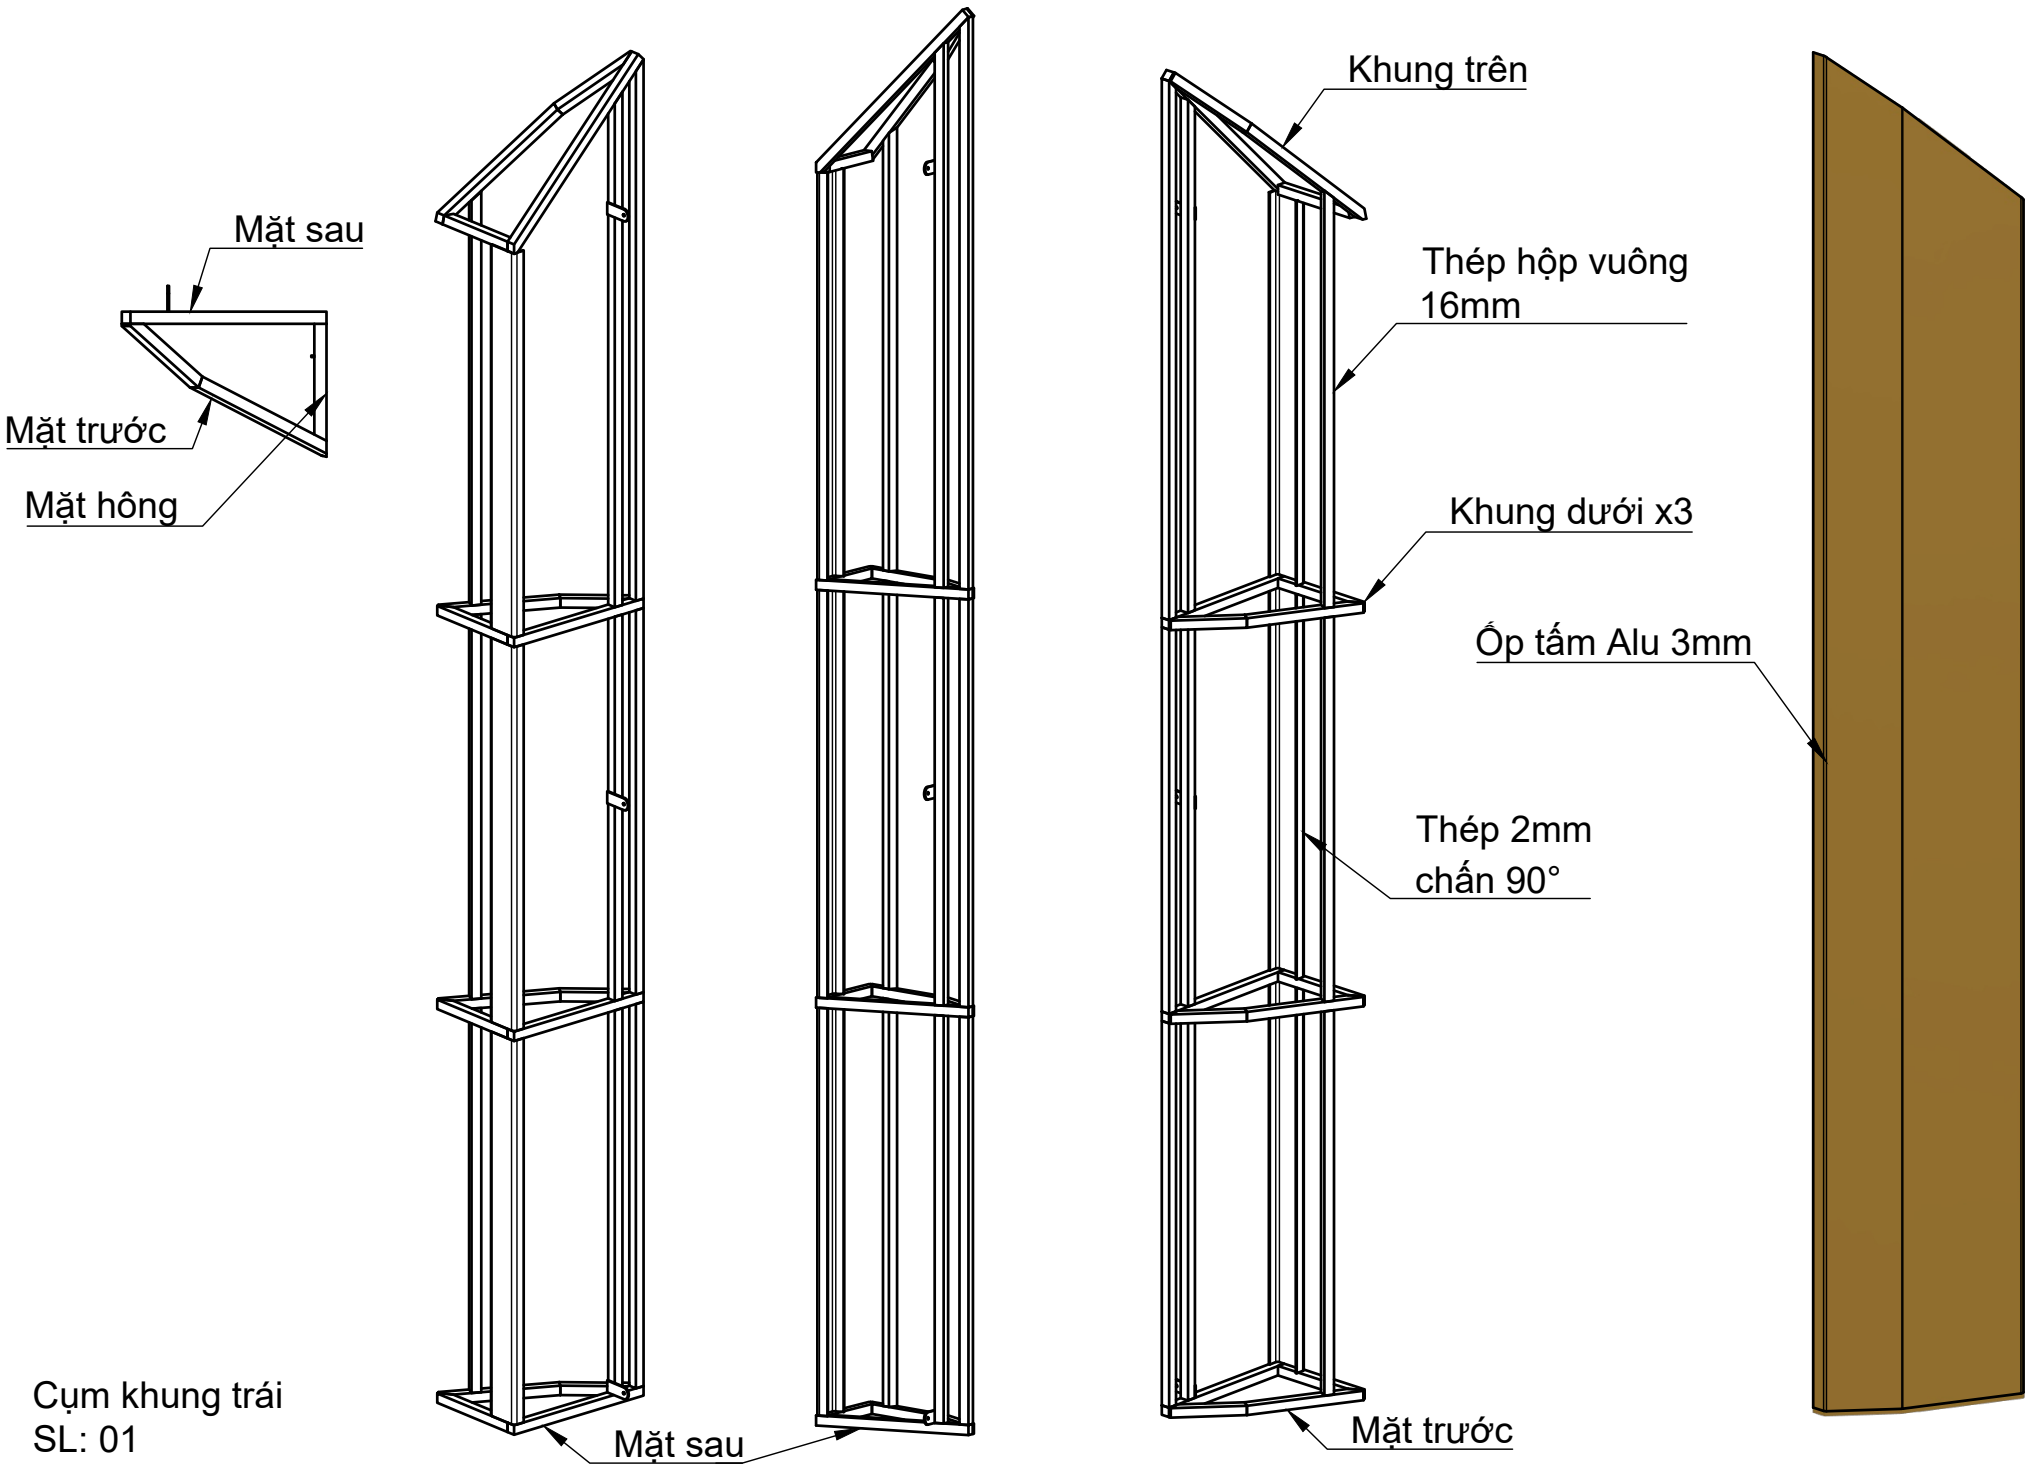


Cụm khung trái
SL: 01

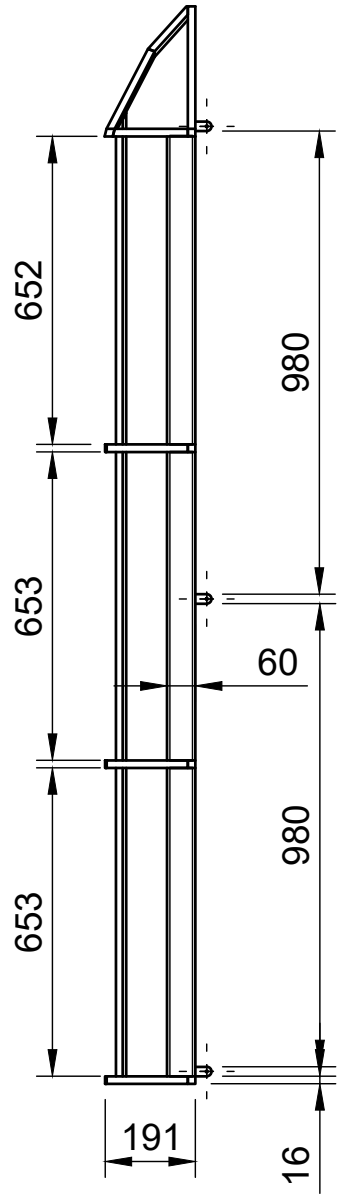

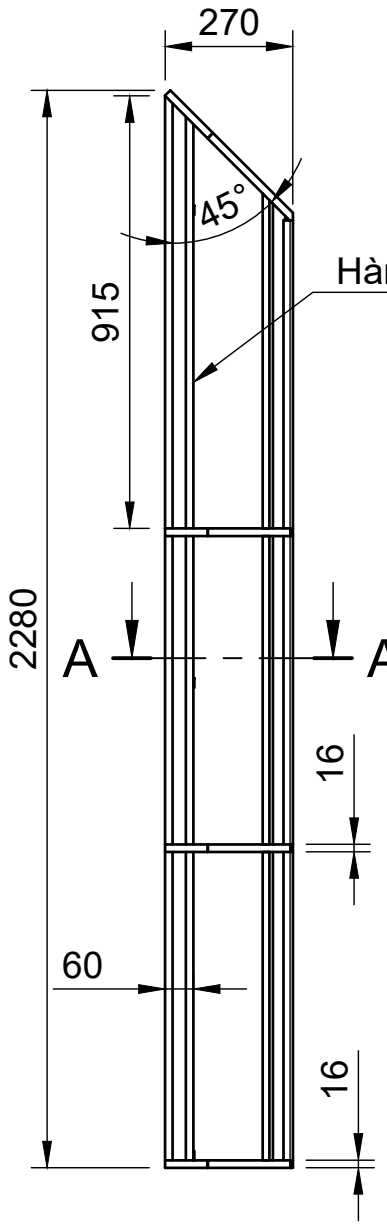

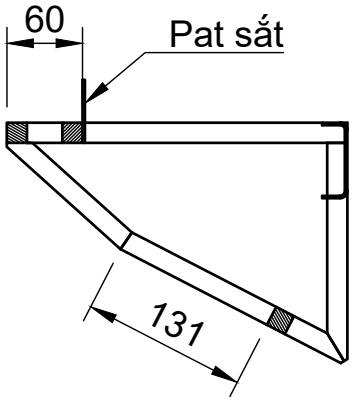


C (1:6)

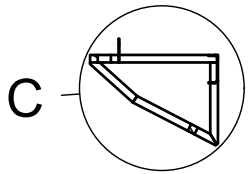


A-A (1:16)


Cụm khung trái
SL: 01

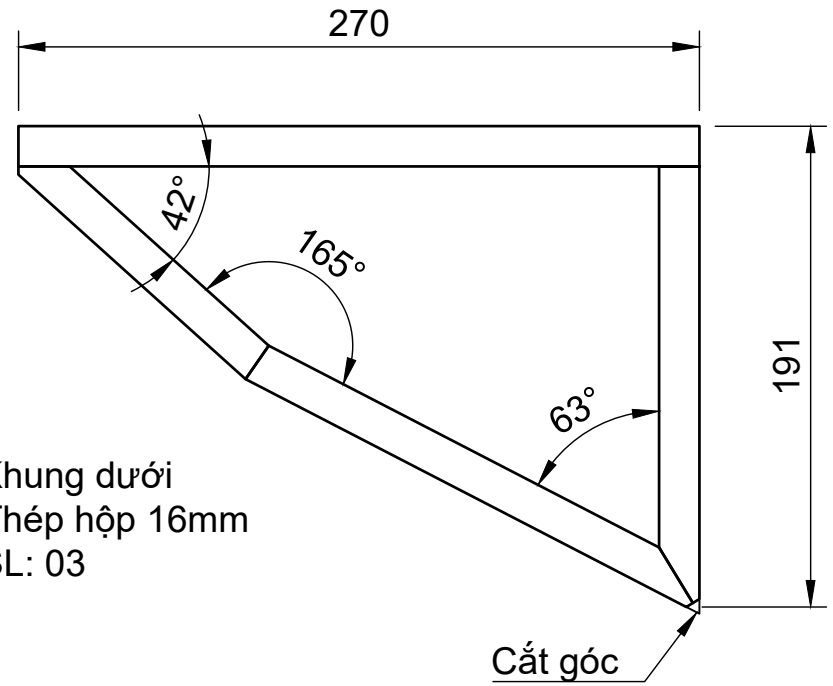


Khung dưới
Thép hộp 16mm
SL: 03

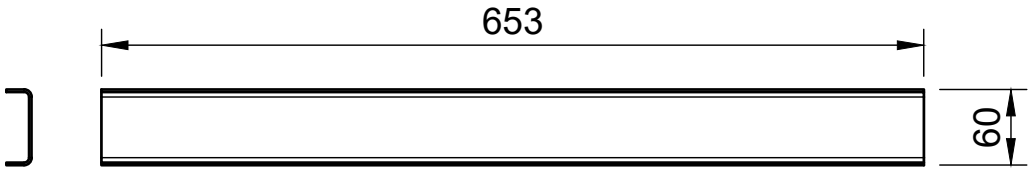


Thanh U
Thép 2mm chấn 90°
SL: 03

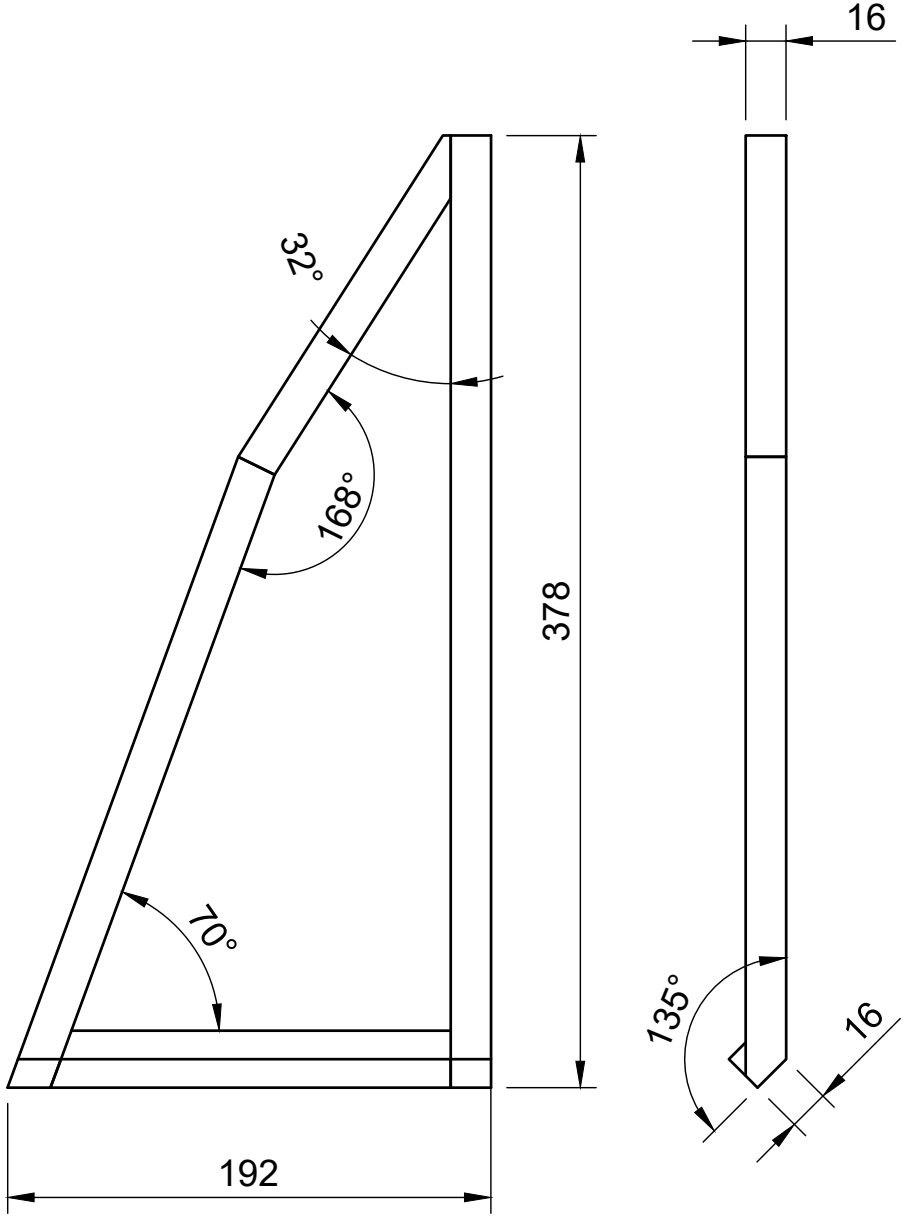



Khung Trên
Thép hộp 16mm
SL: 01

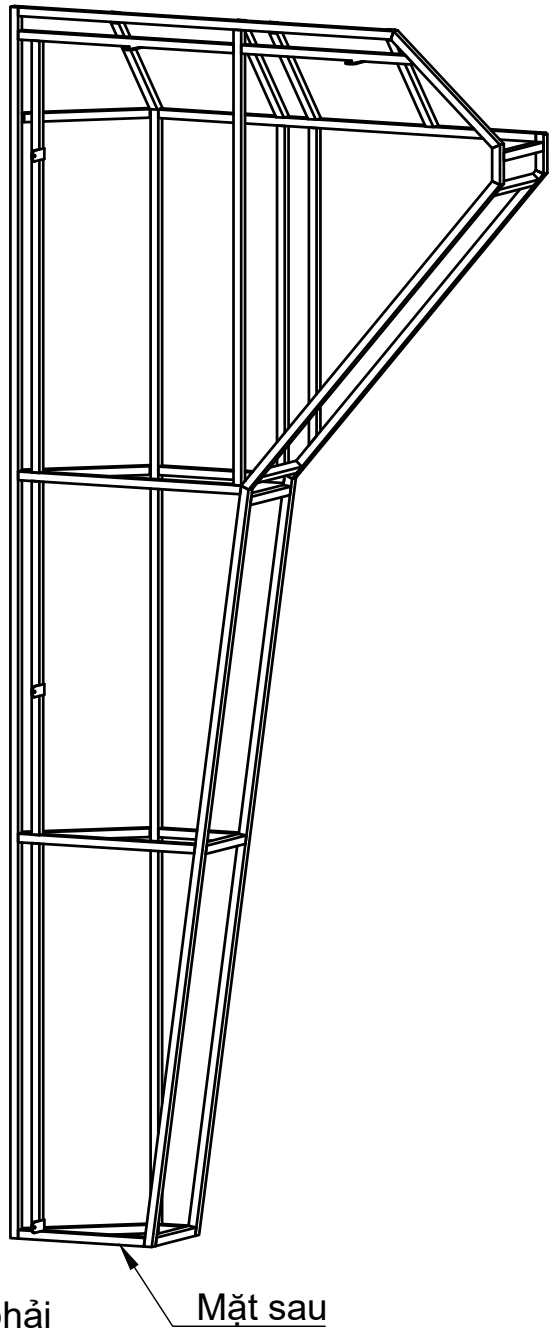


Cụm khung phải
SL: 01

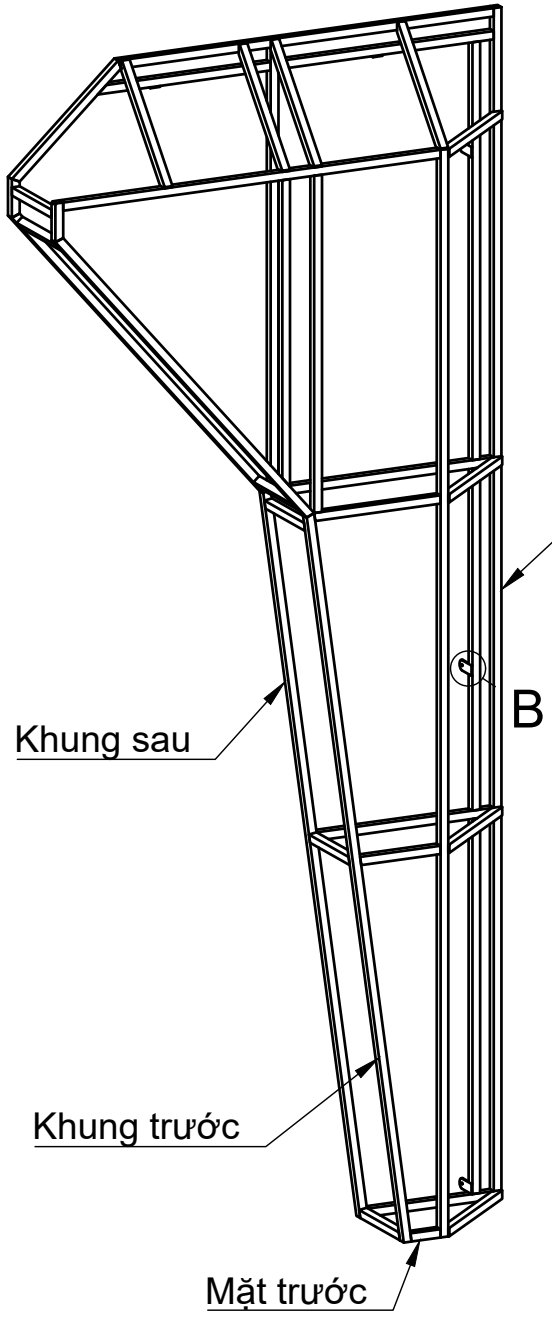

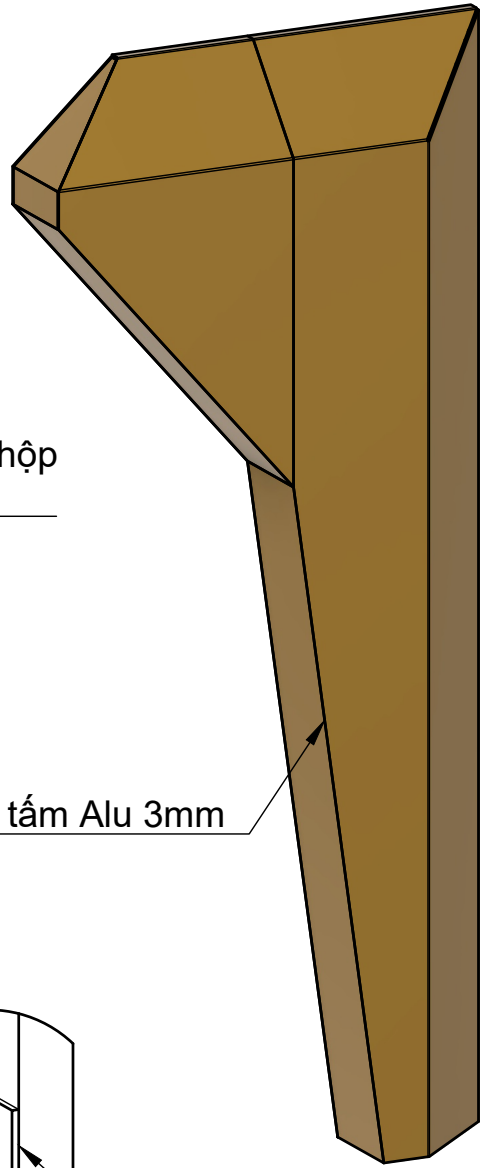


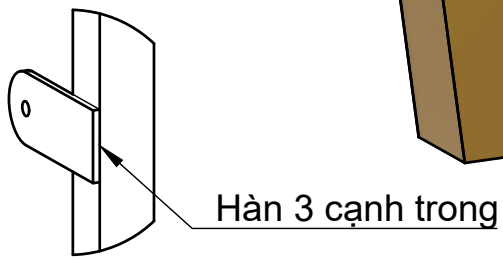


B (1:2)

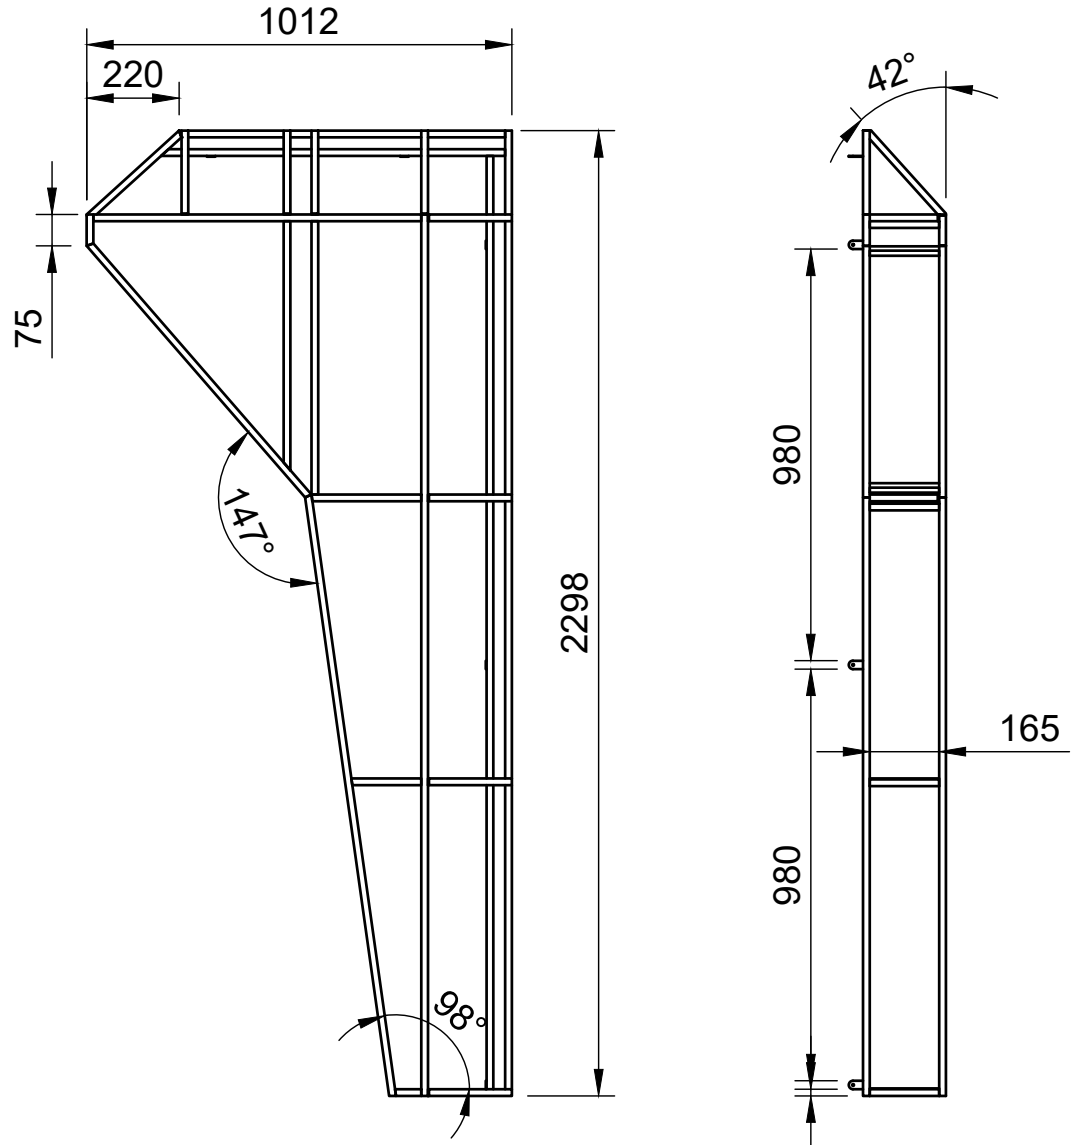


Cụm khung phải
SL: 01

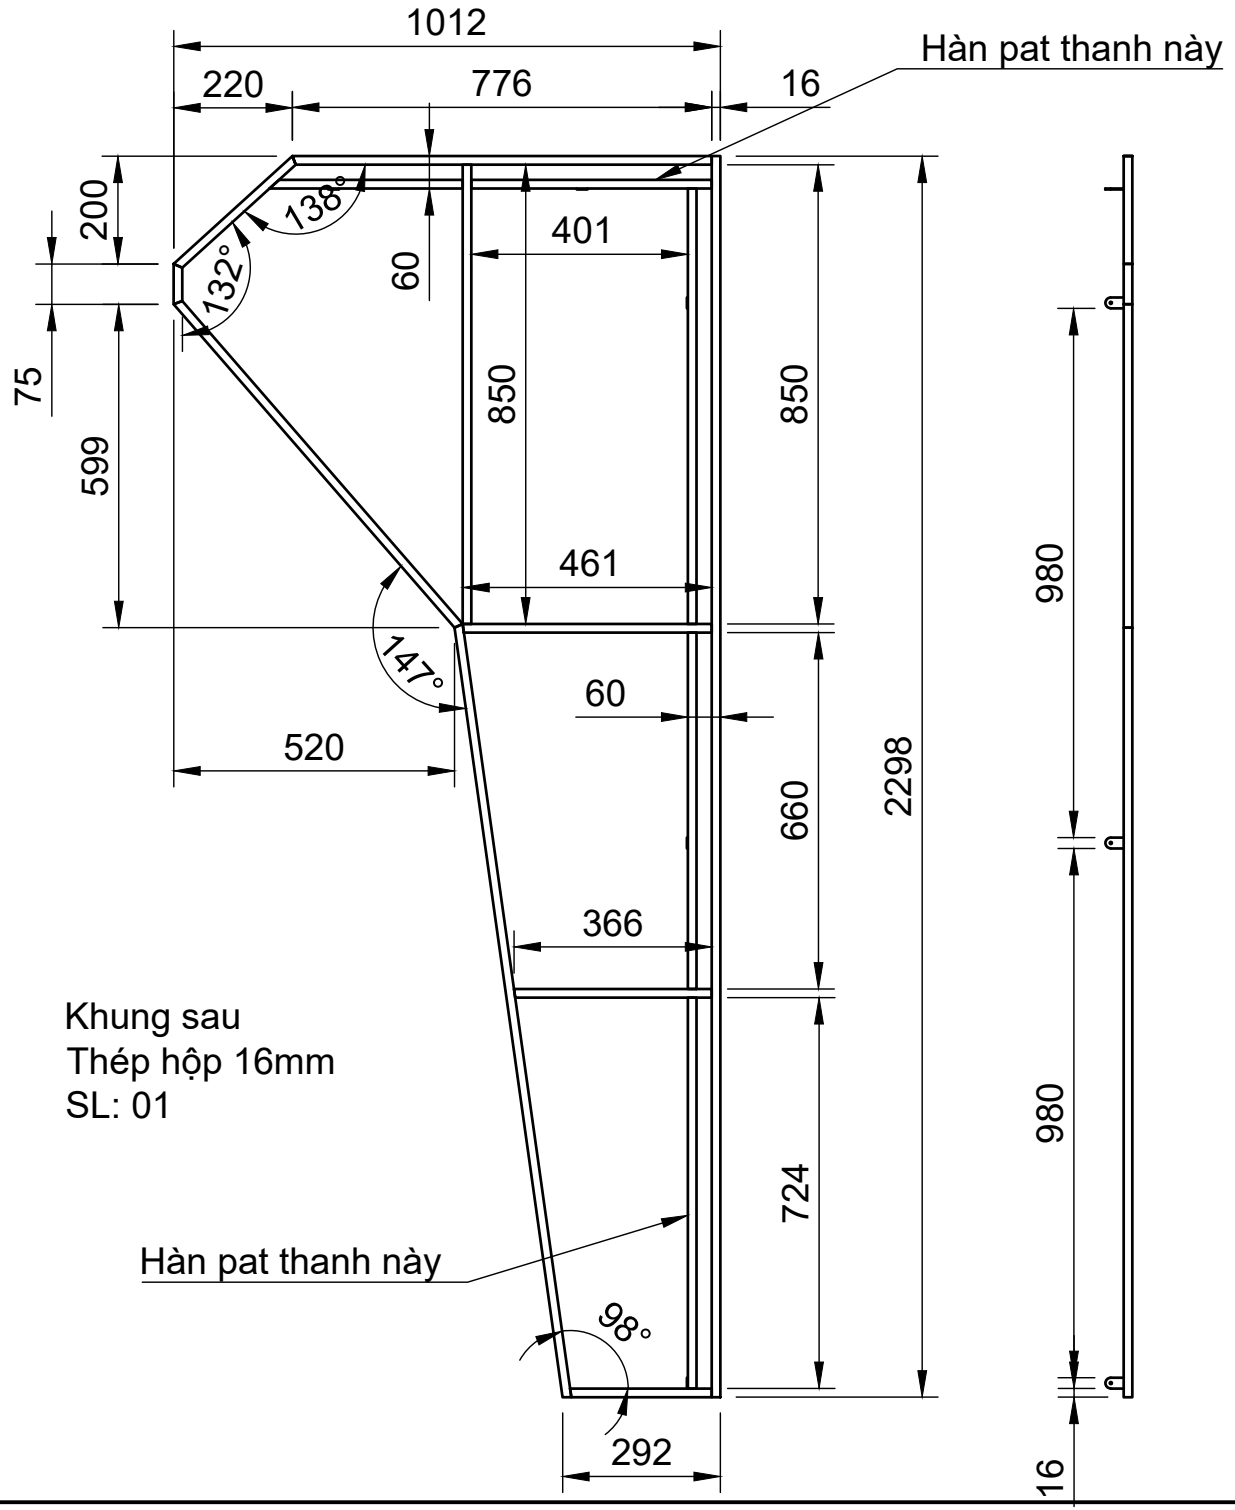



Khung sau
Thép hộp 16mm
SL: 01

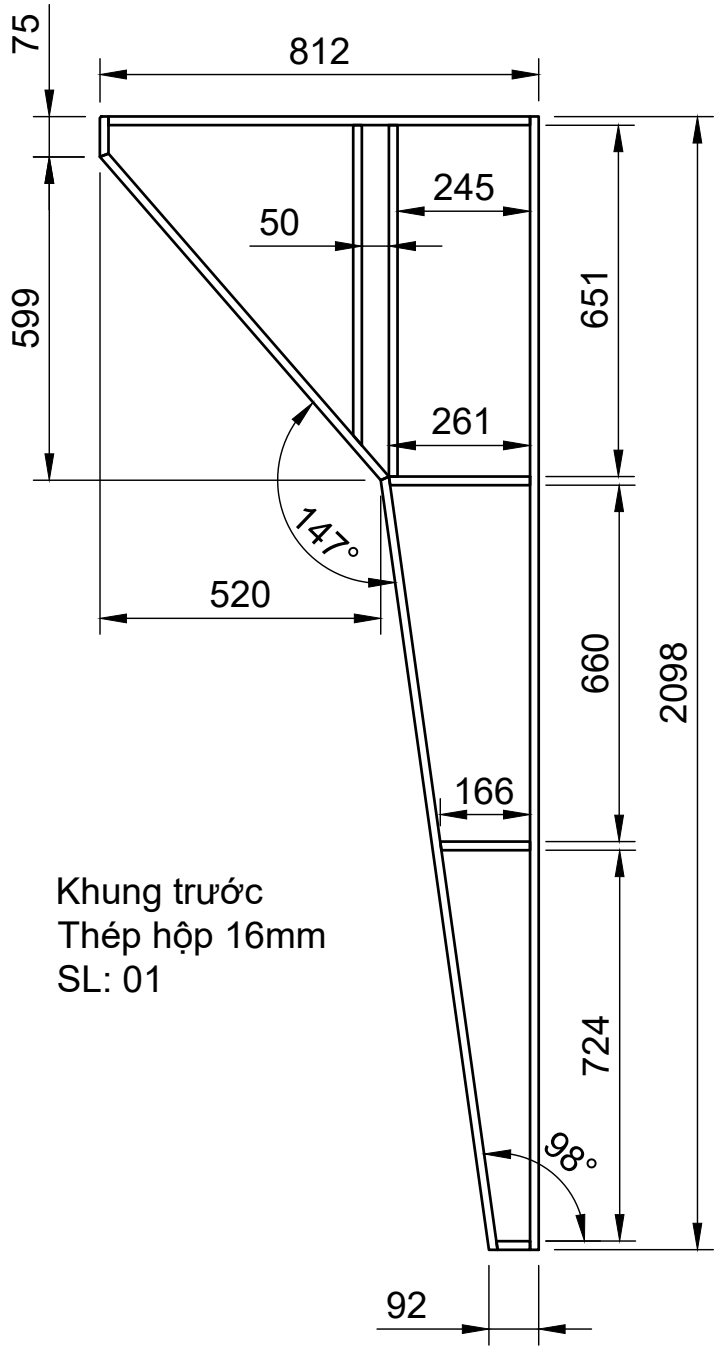


Khung trước
Thép hộp 16mm
SL: 01

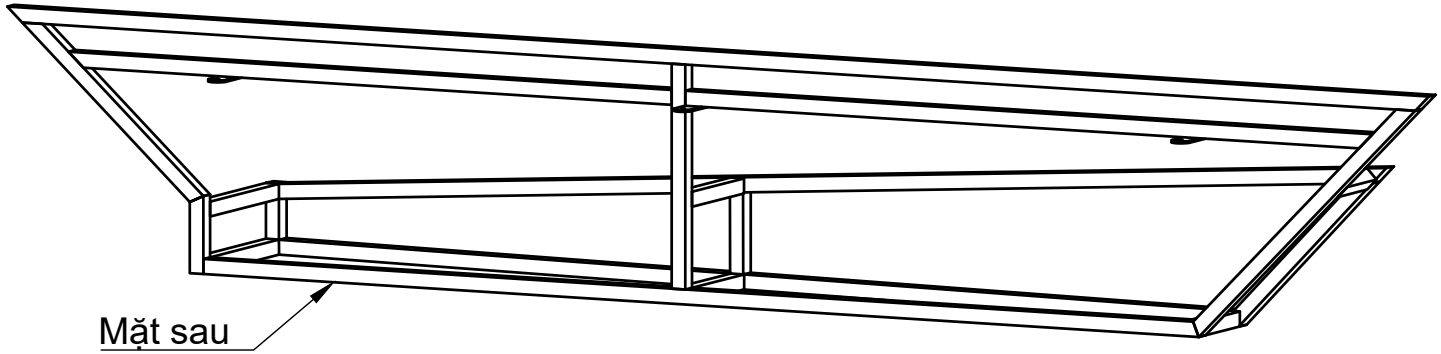

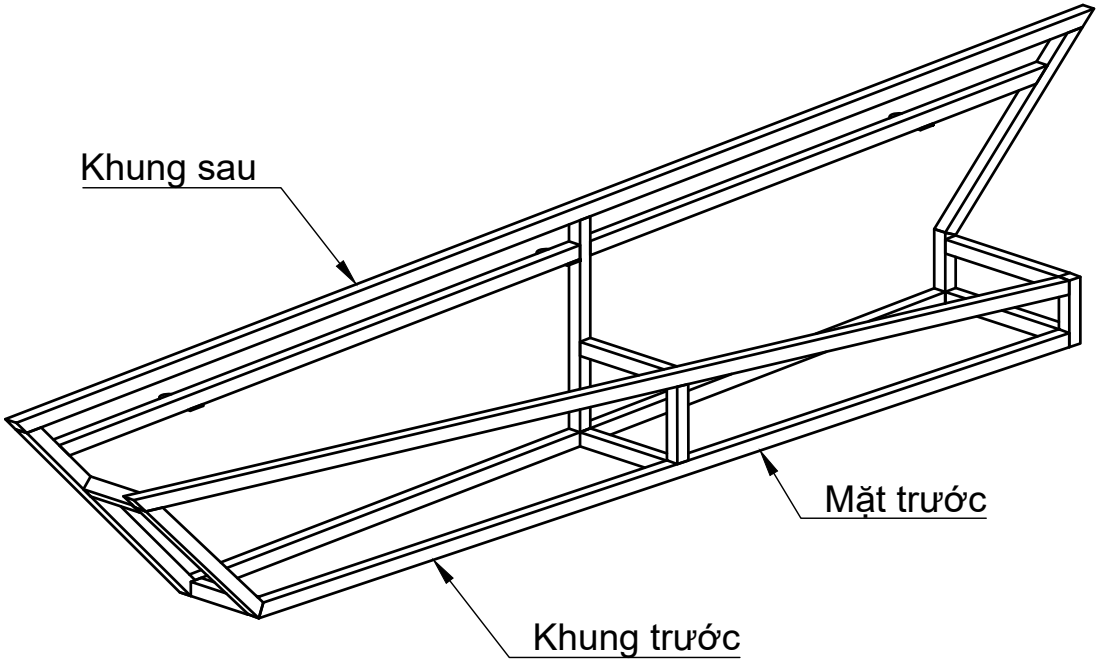


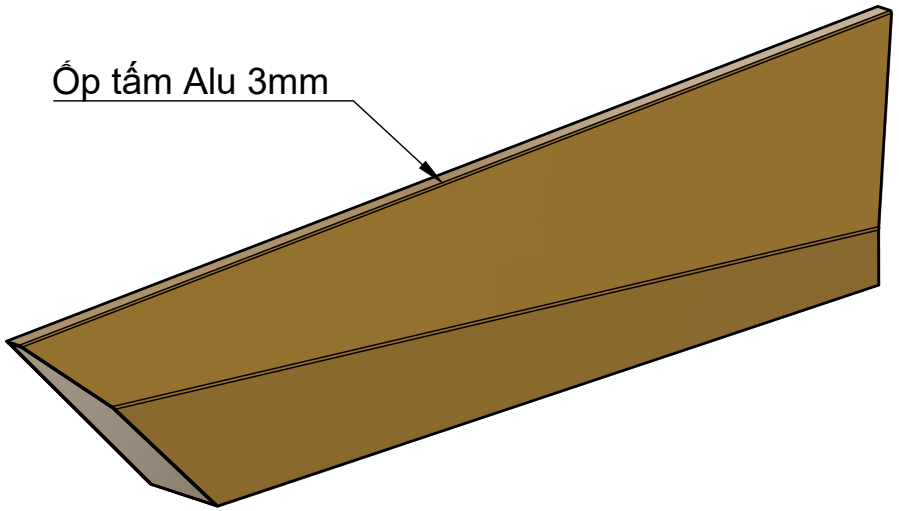


Cụm khung trên
SL: 01

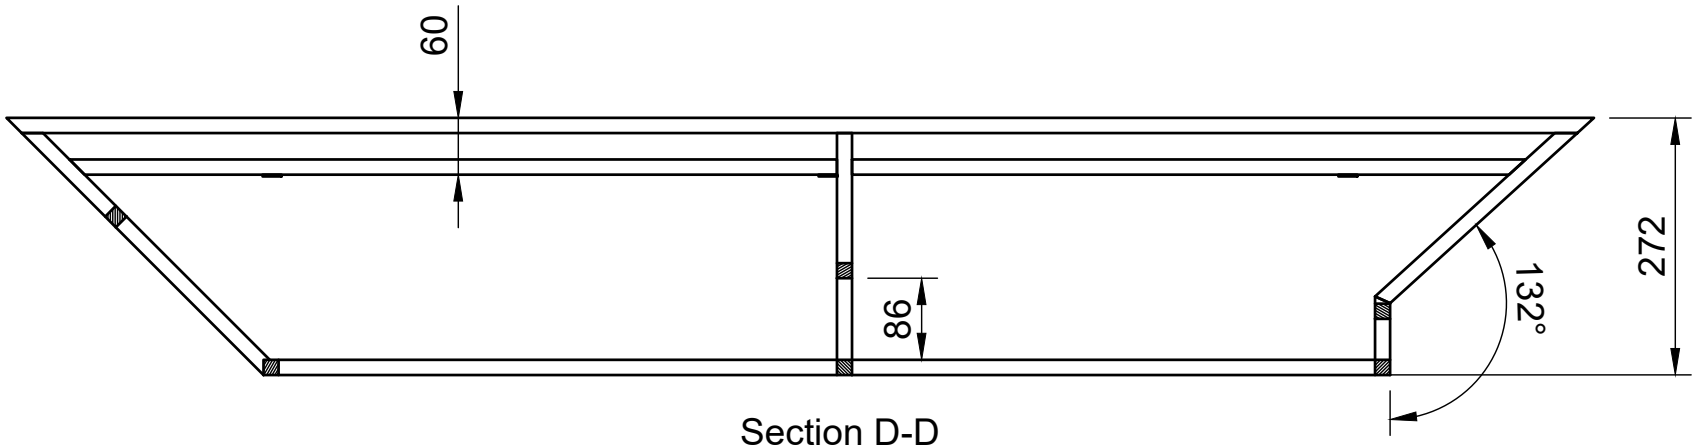


Section D-D

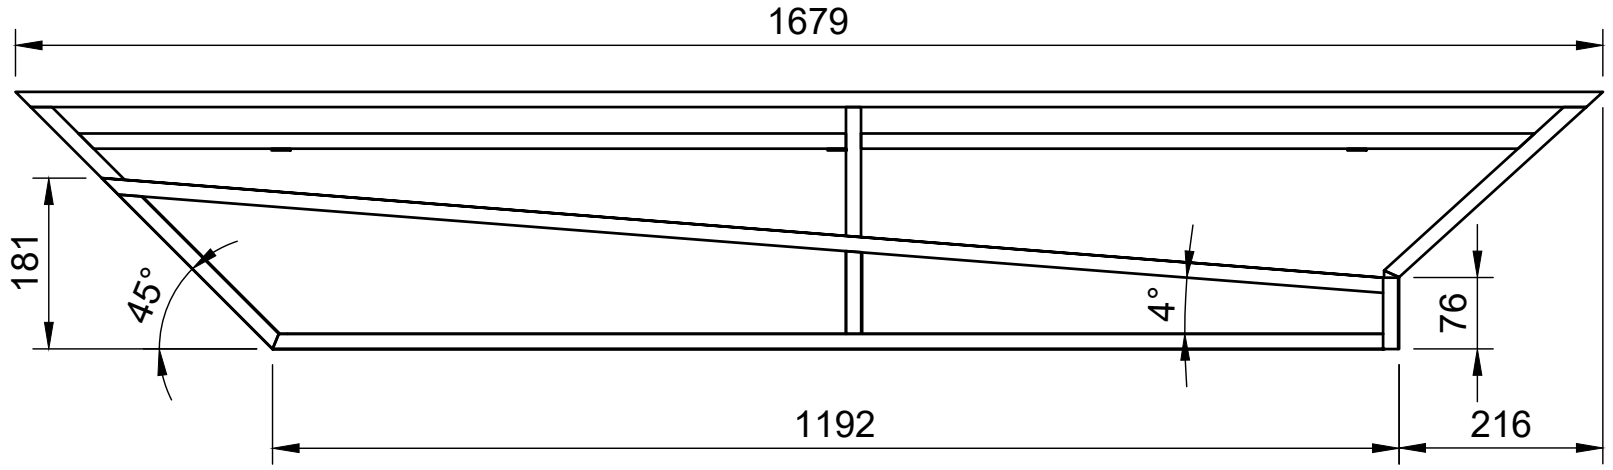


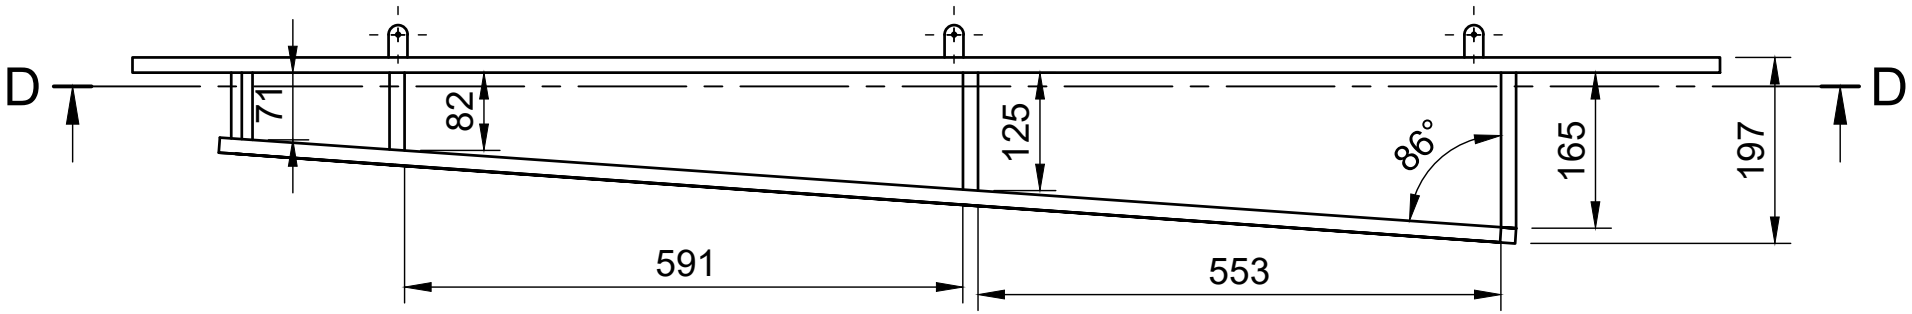

Cụm khung trên
SL: 01

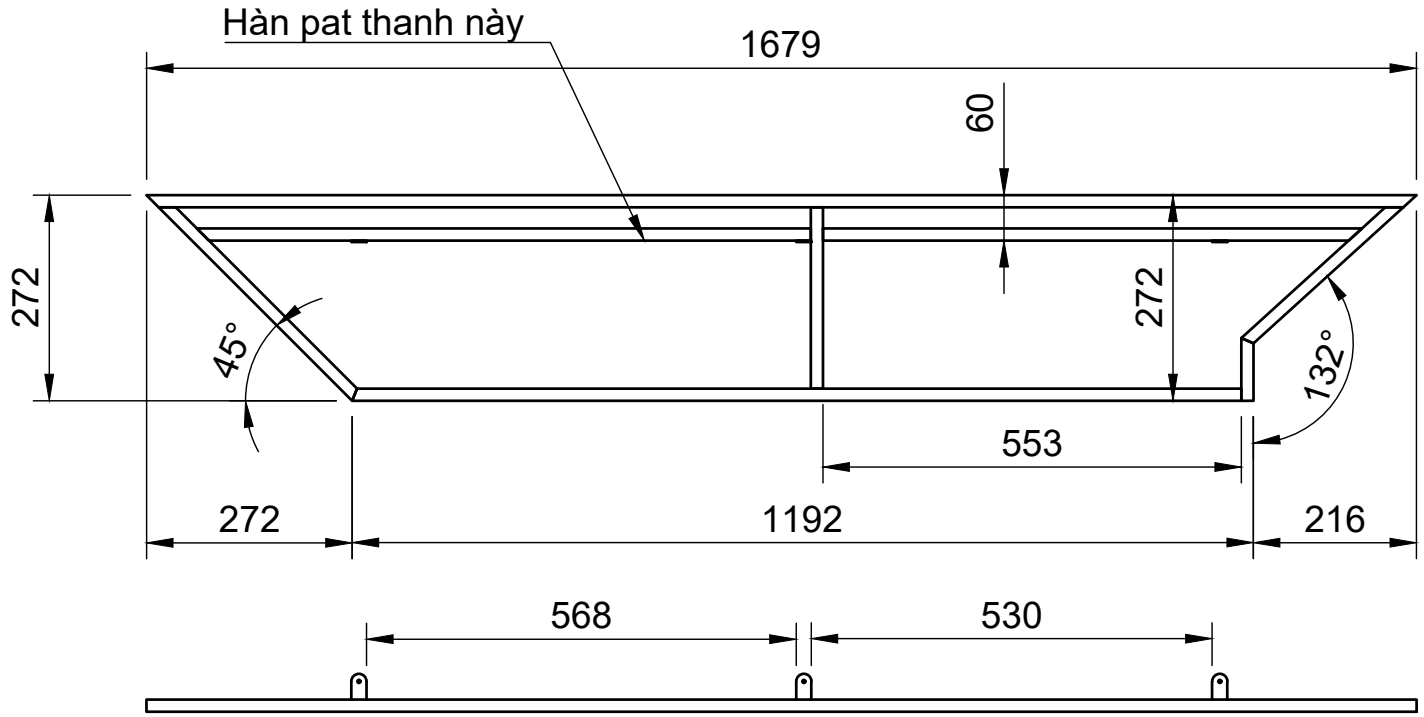



Khung sau
Thép hộp 16mm
SL: 01

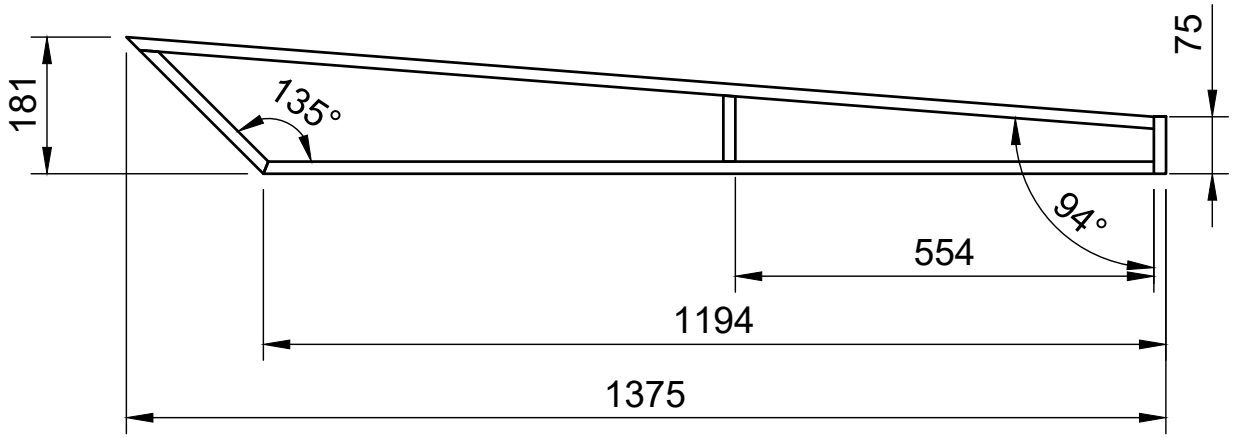


Khung trước
Thép hộp 16mm
SL: 01

Pat sắt
Thép dày 2mm
SL: 11pcs

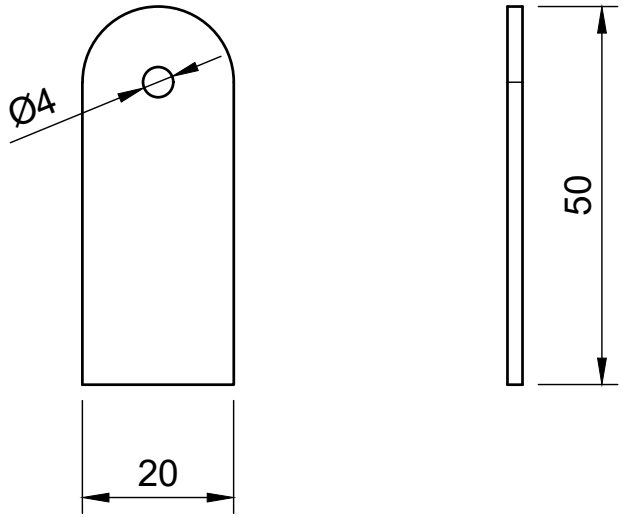


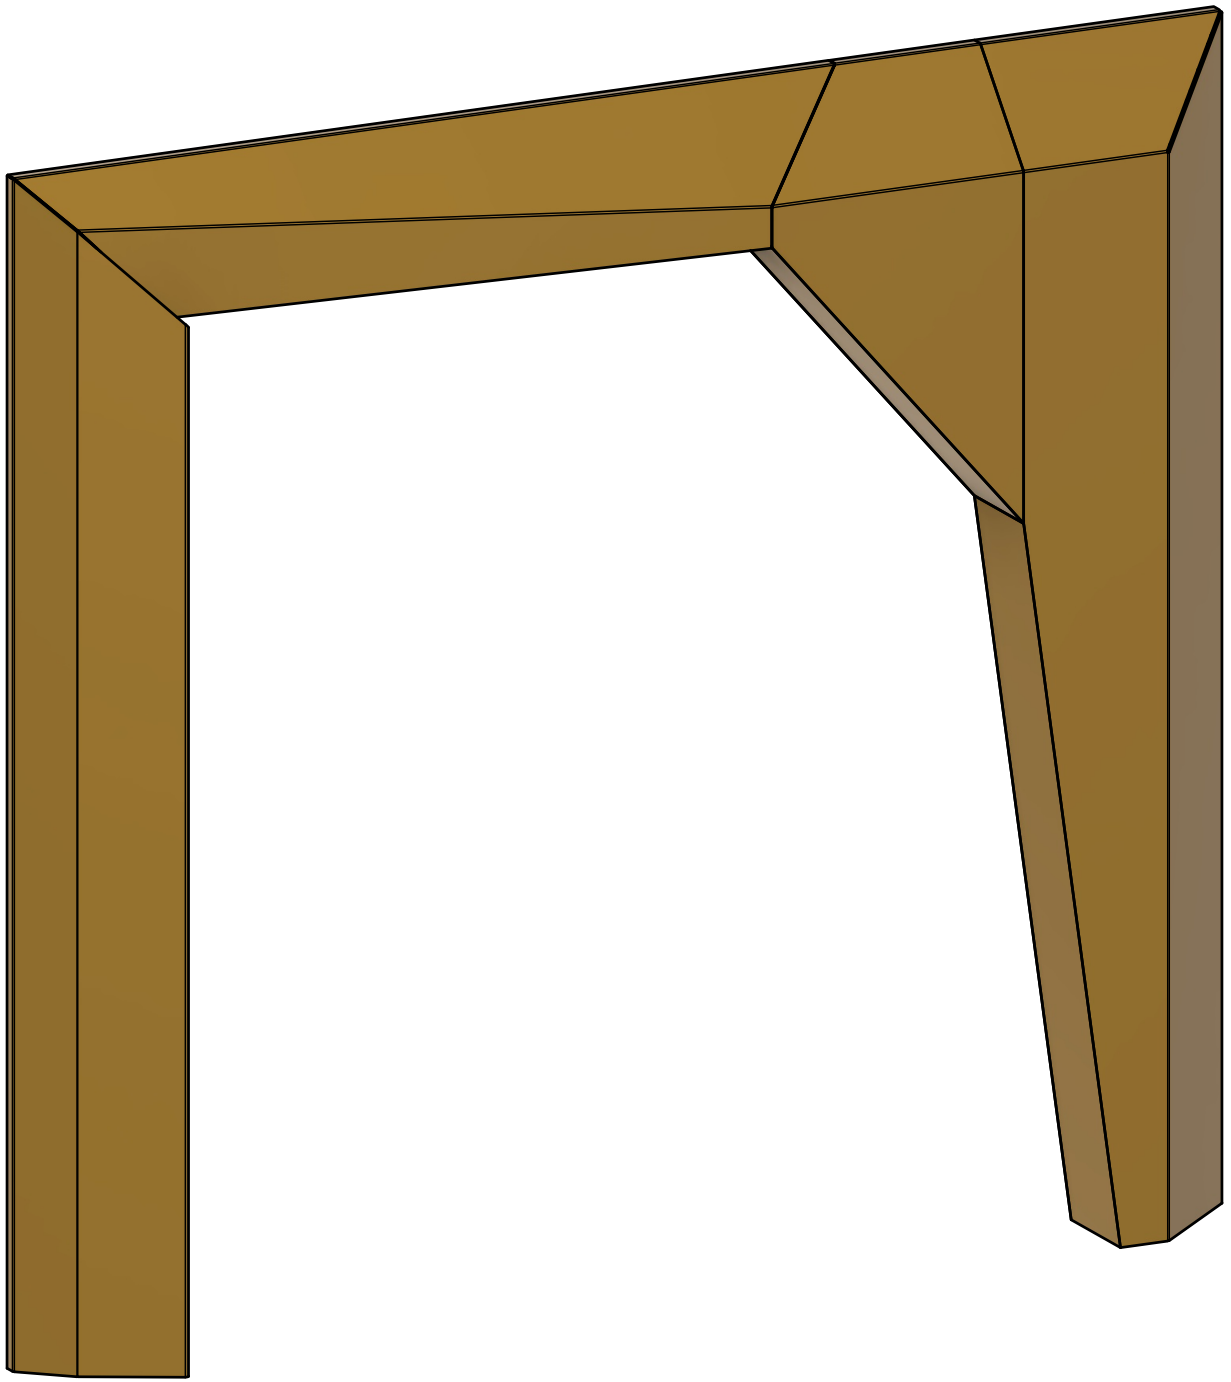


Cụm trang trí

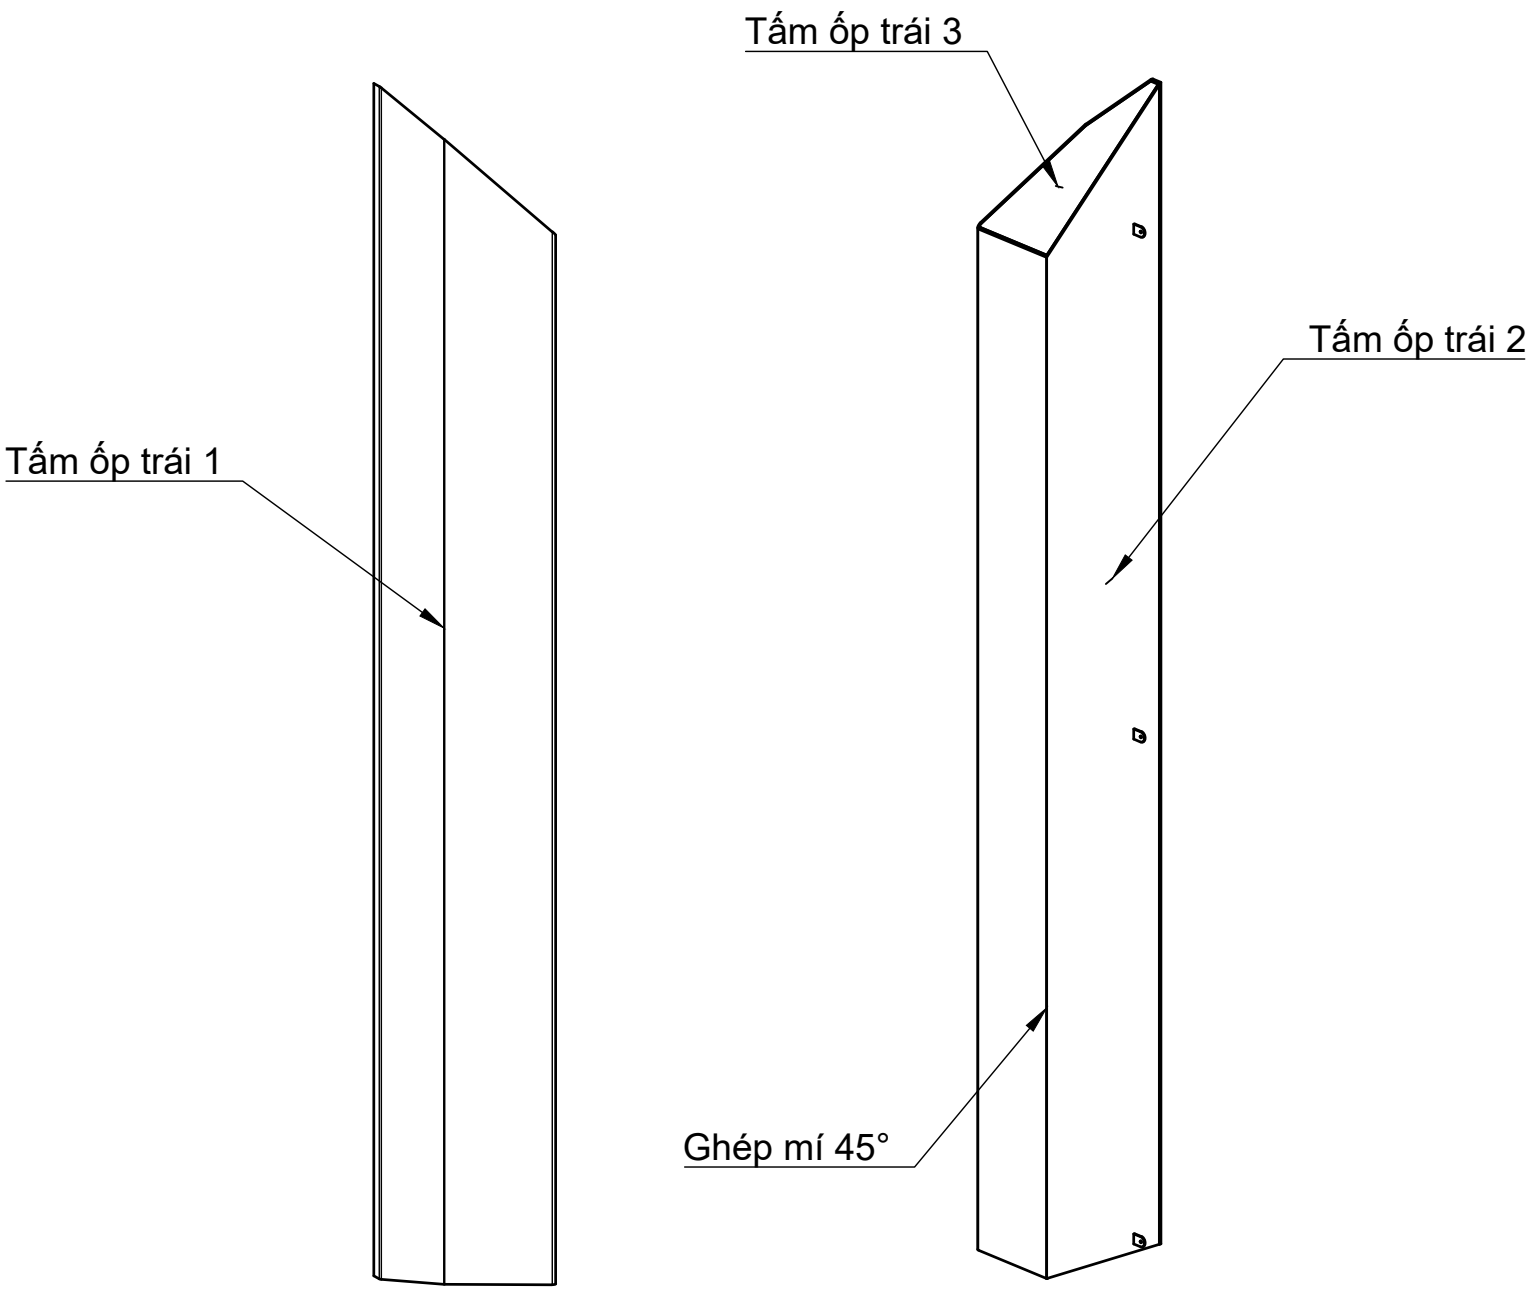

Cụm trái

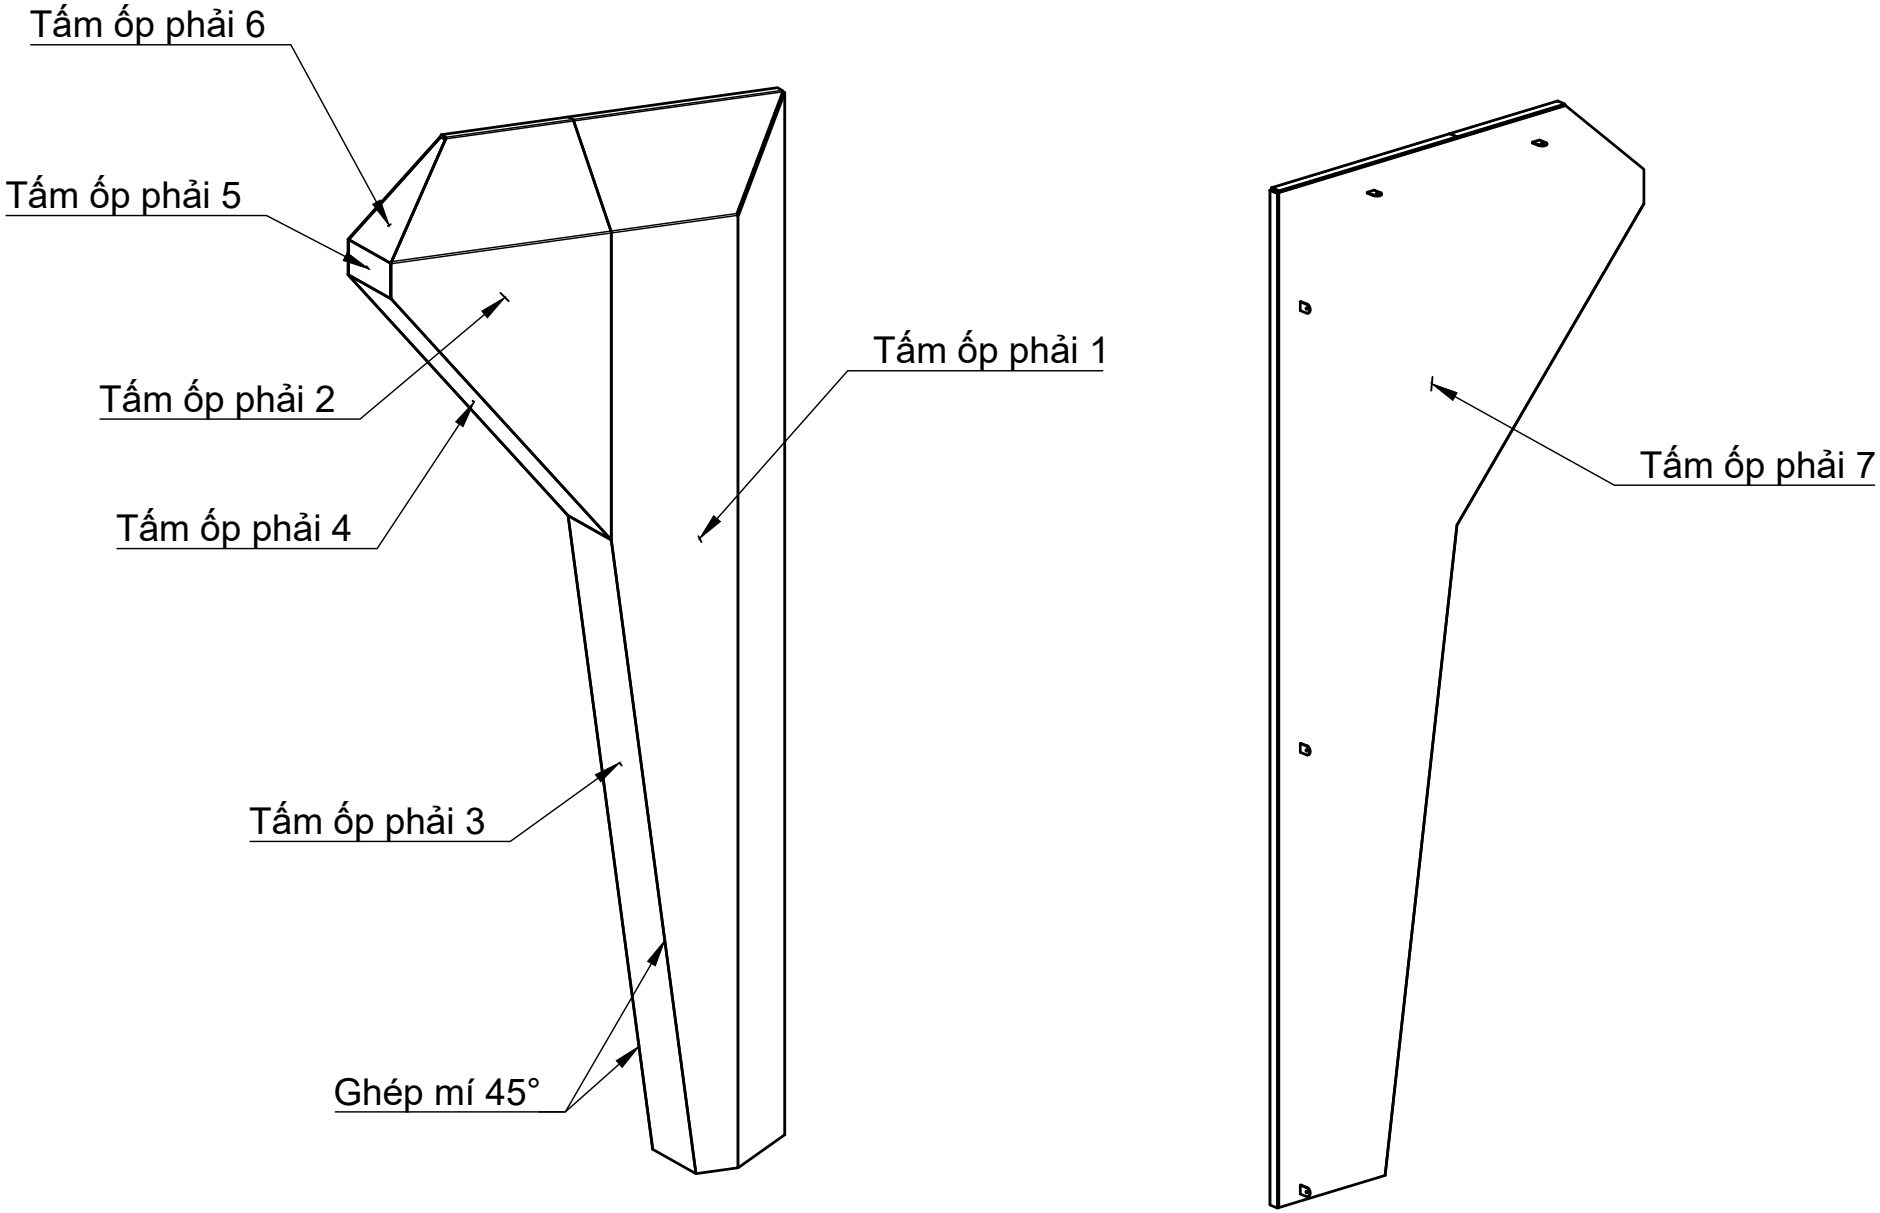
Tấm ốp phải 6
Tấm ốp phải 5
Tấm ốp phải 2
Tấm ốp phải 4
Tấm ốp phải 3
Ghép mí 45°
Tấm ốp phải 1
Tấm ốp phải 7

Cụm phải

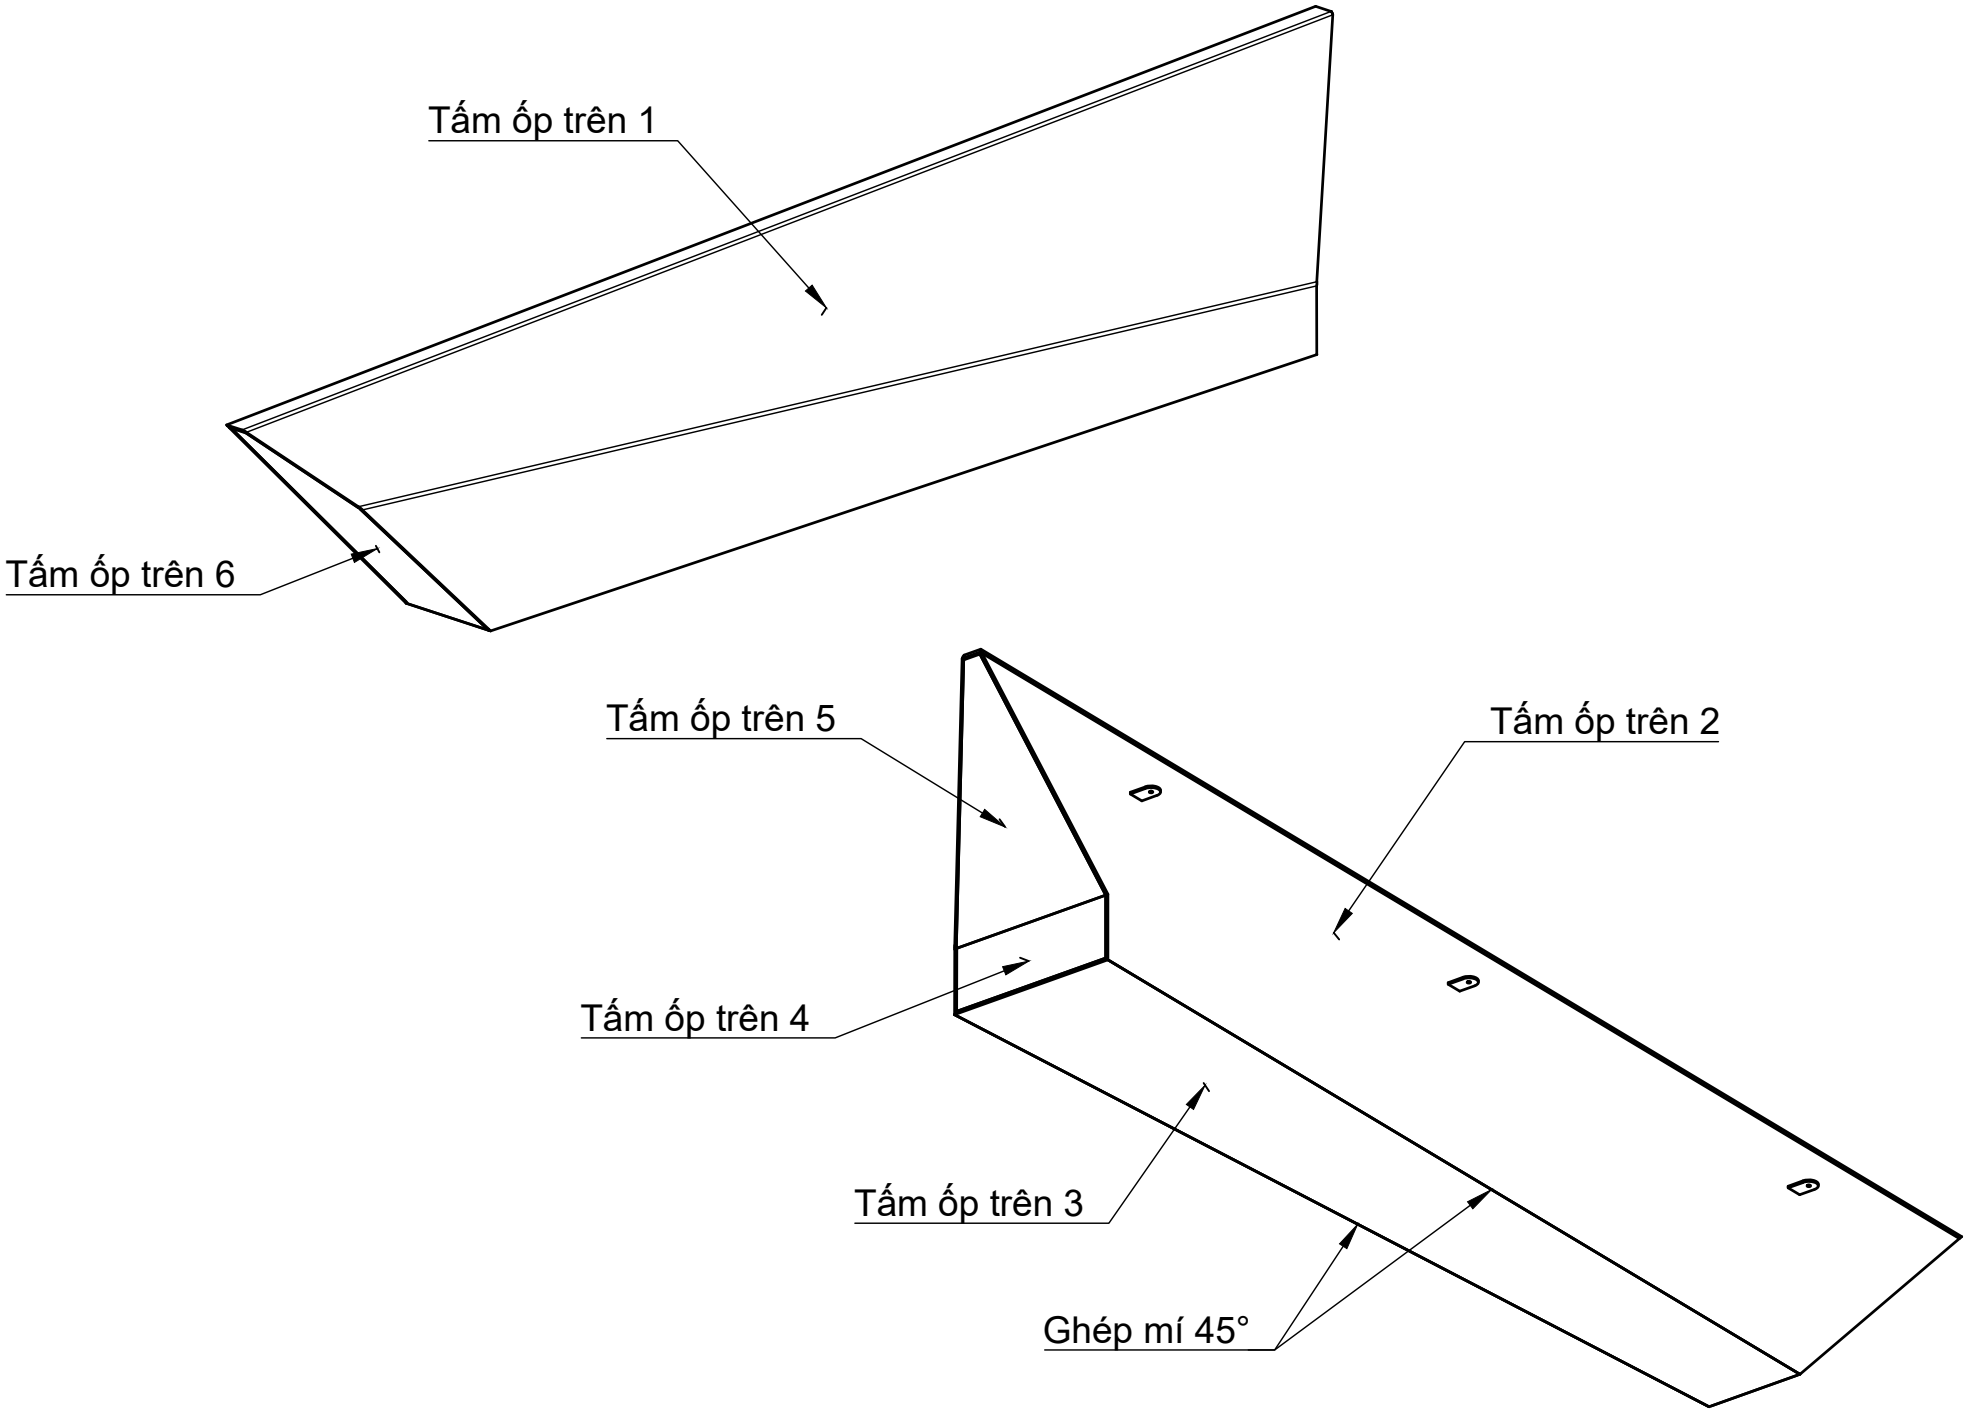
Tấm ốp trên 1
Tấm ốp trên 6
Tấm ốp trên 5
Tấm ốp trên 2
Tấm ốp trên 4
Tấm ốp trên 3
Ghép mí 45°

Cụm trên