



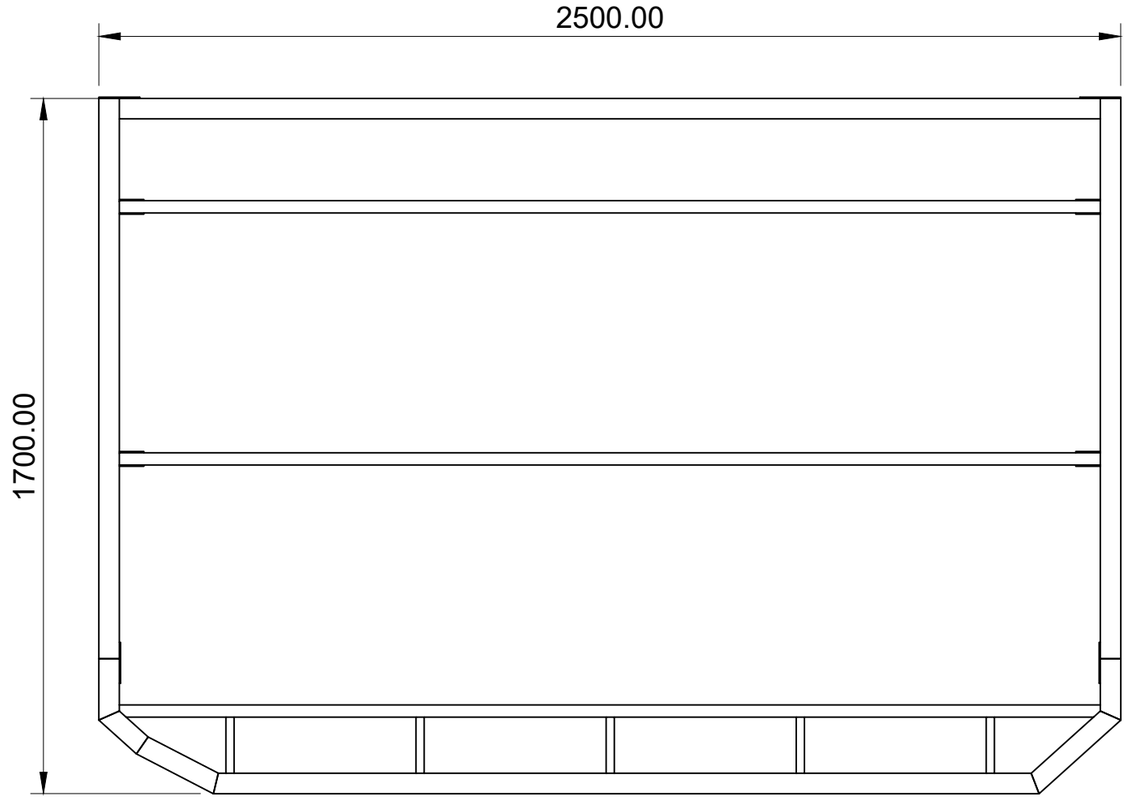


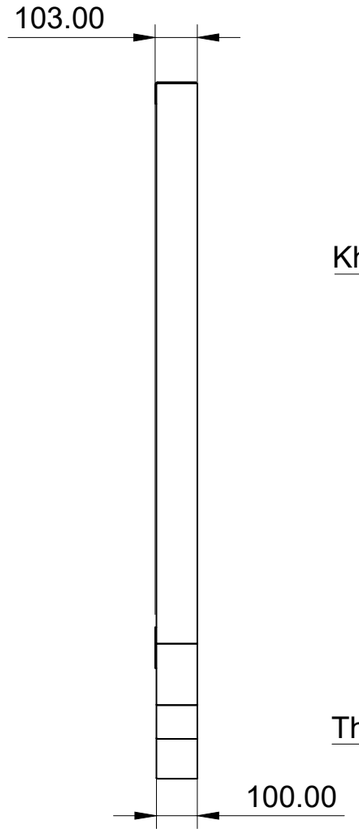


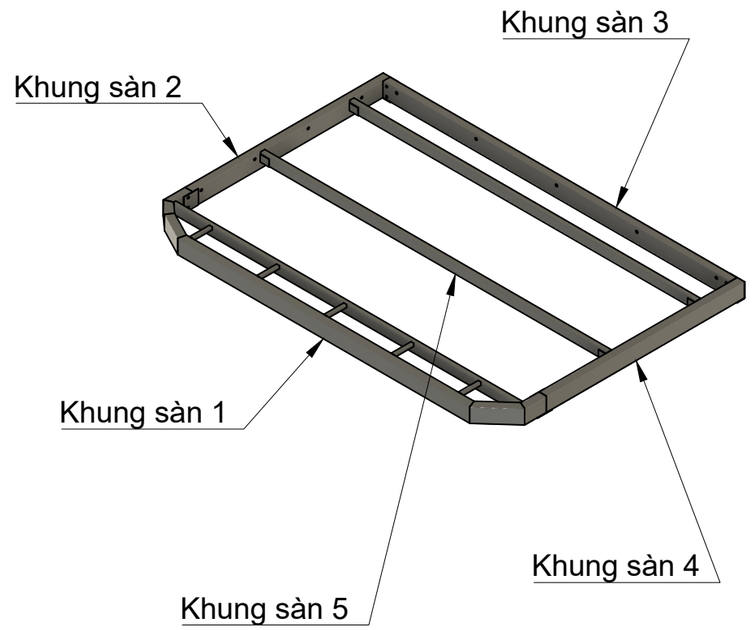


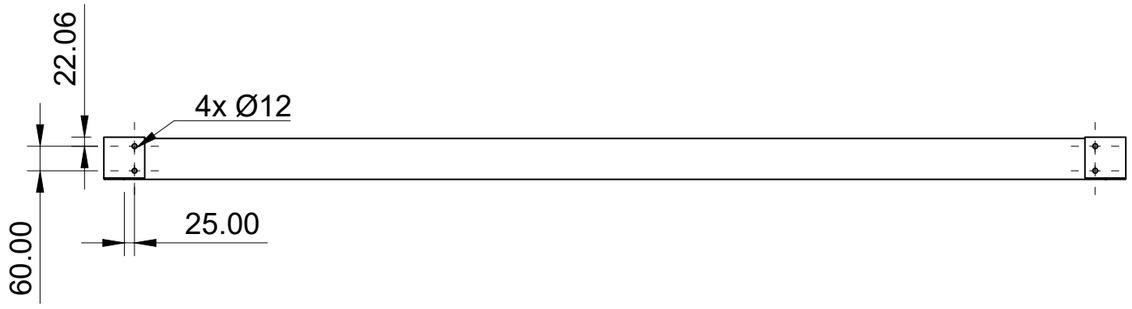


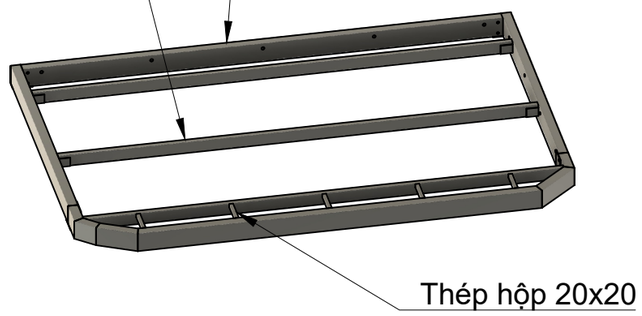



Title	Sheet
Khung sàn	1/8

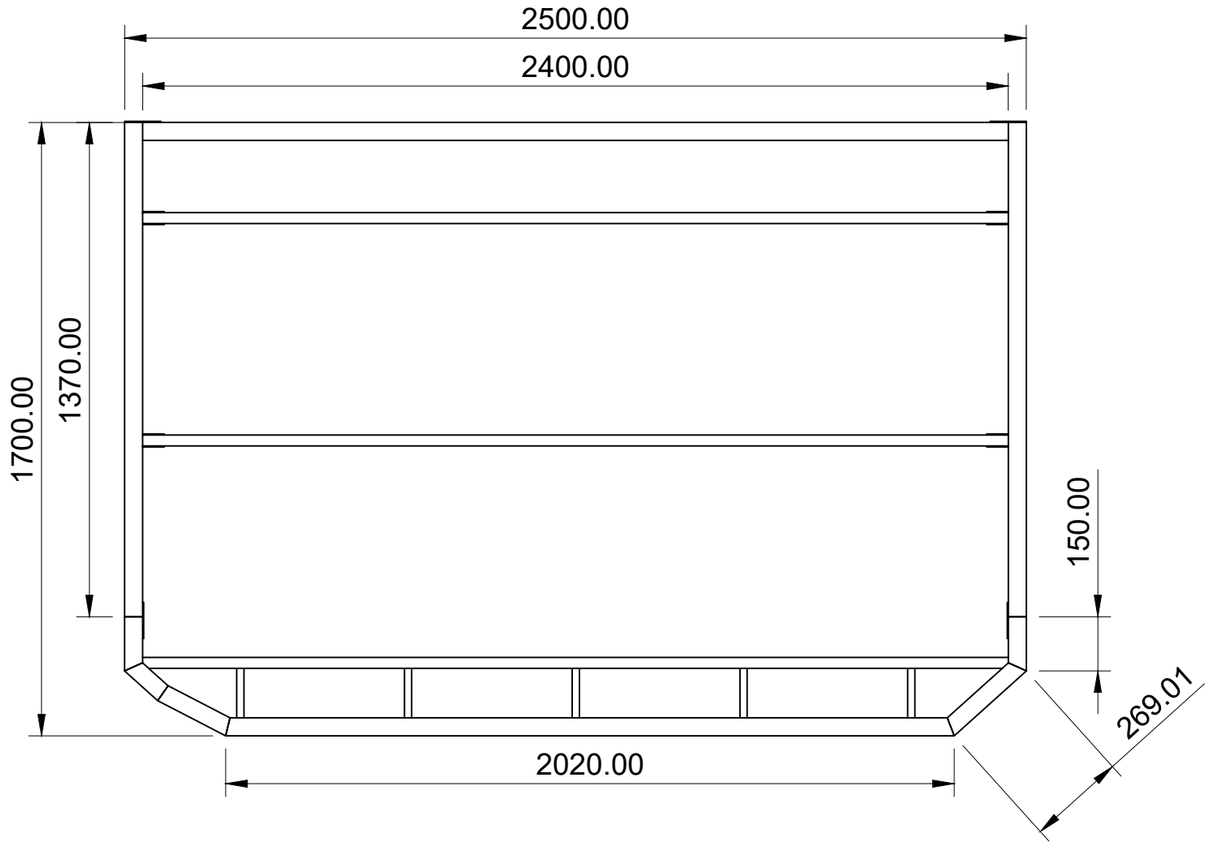


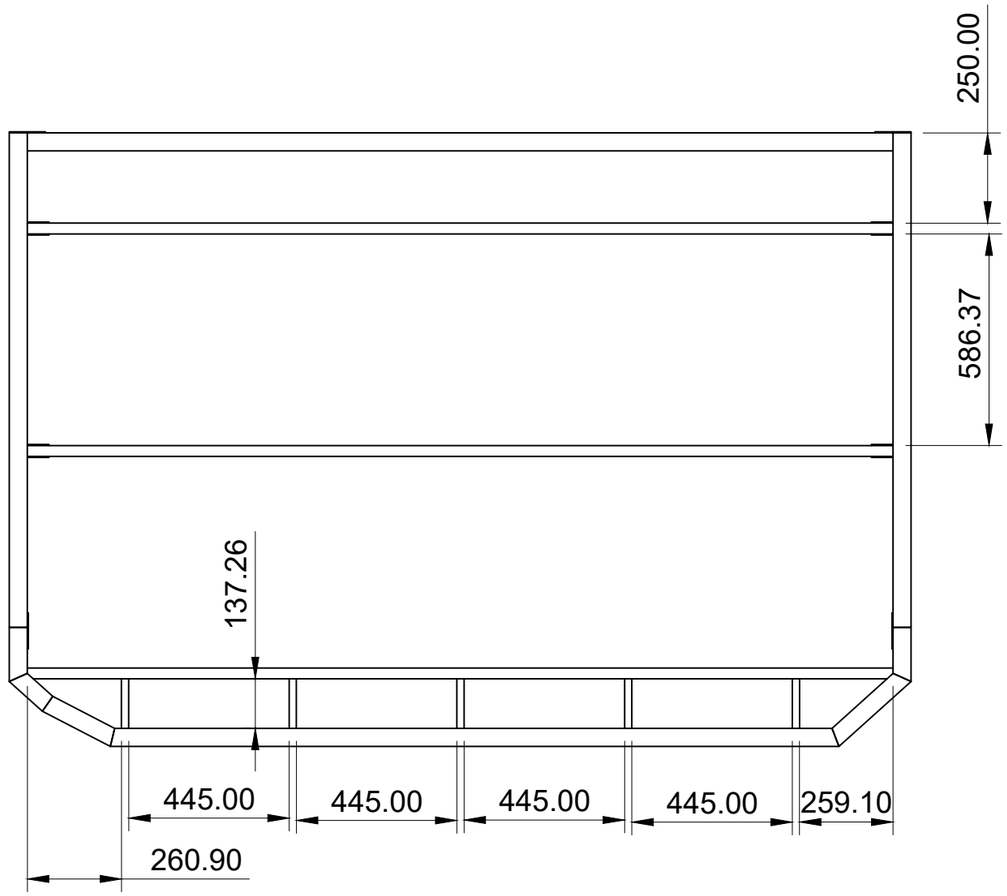

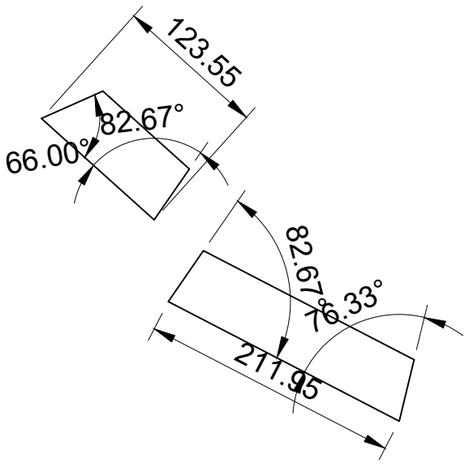


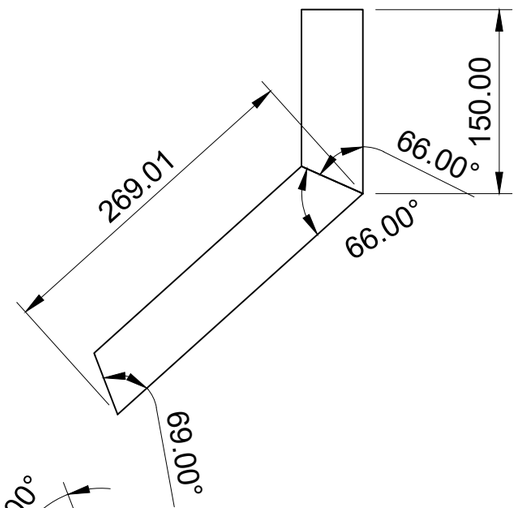


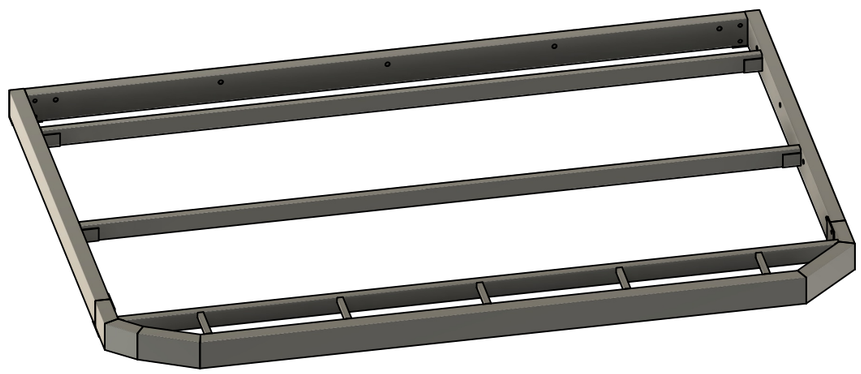


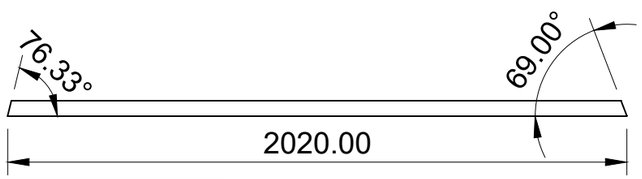


Title	Sheet
Khung sàn	2/8

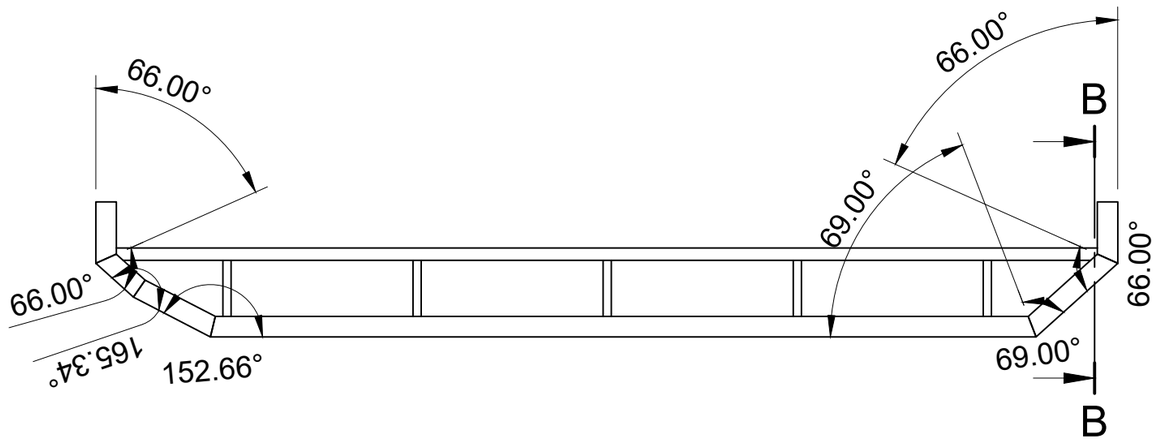

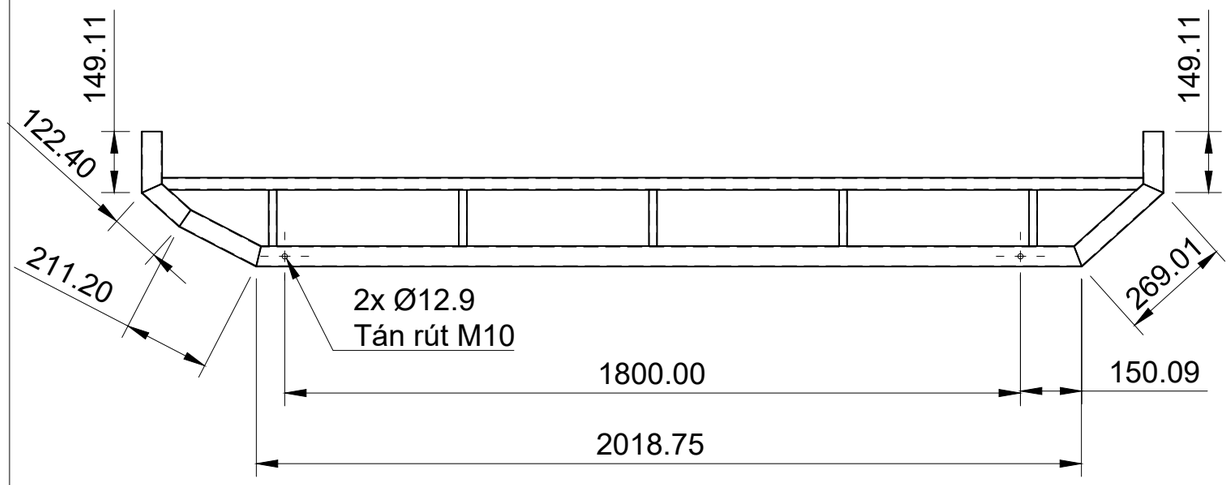


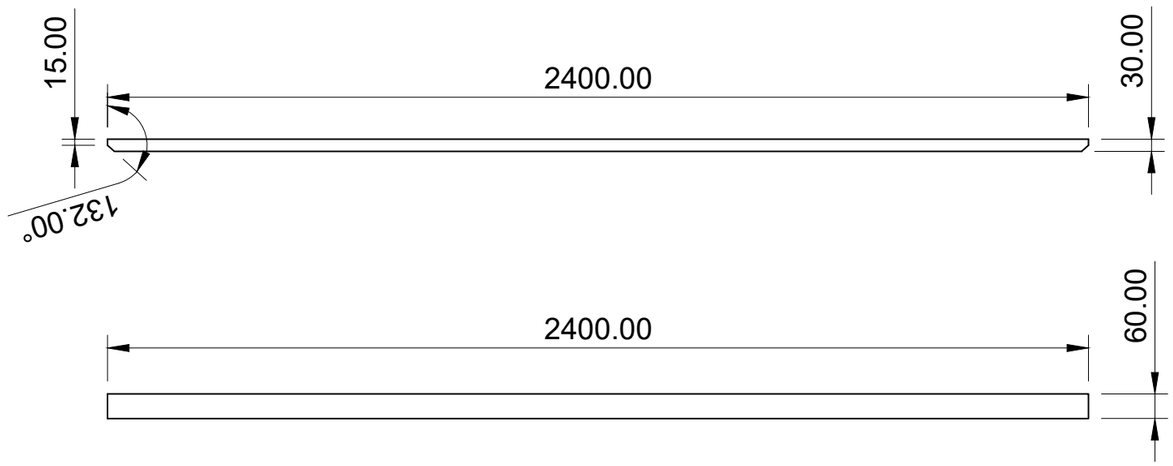


B-B (1:8)

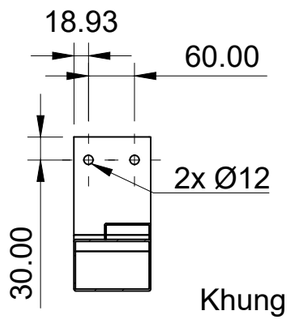



D (1:9)

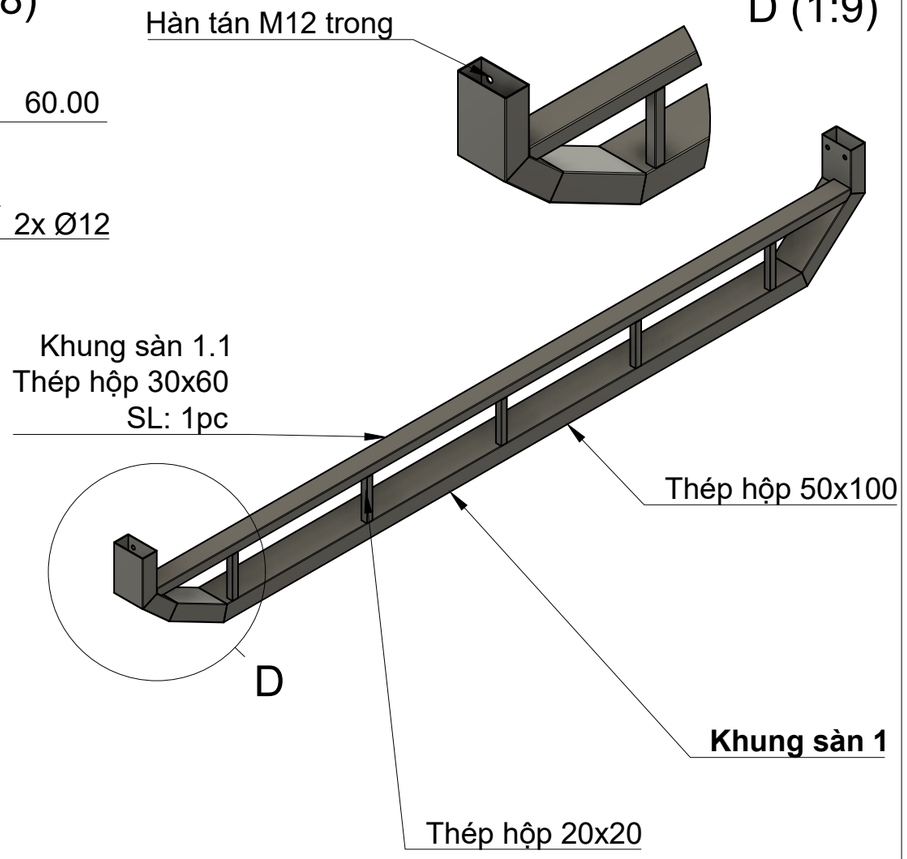


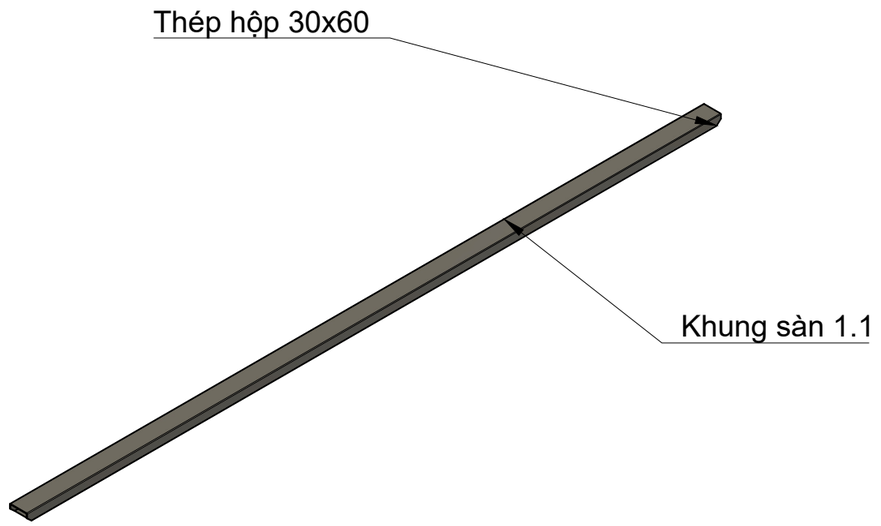



Title	Sheet
Khung sàn_1 SL: 1	3/8

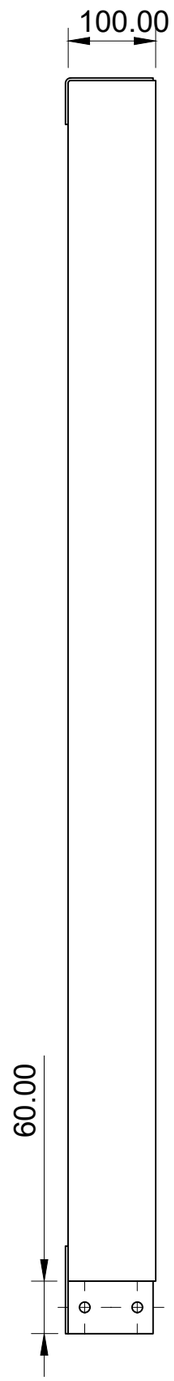


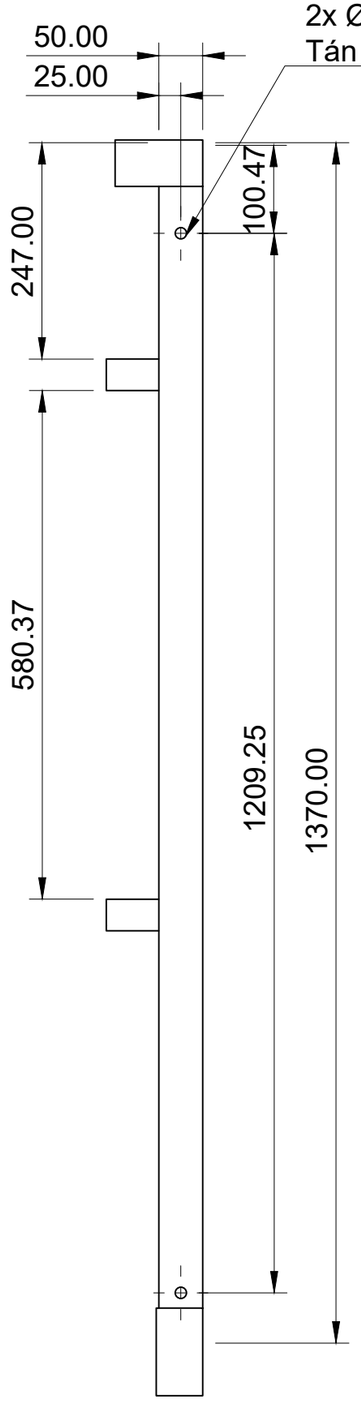


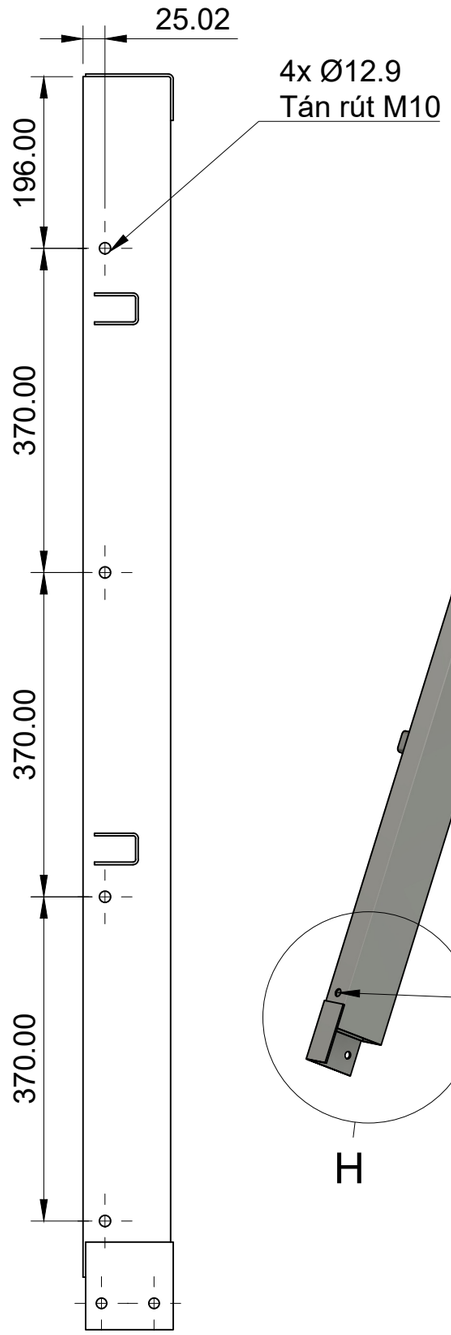


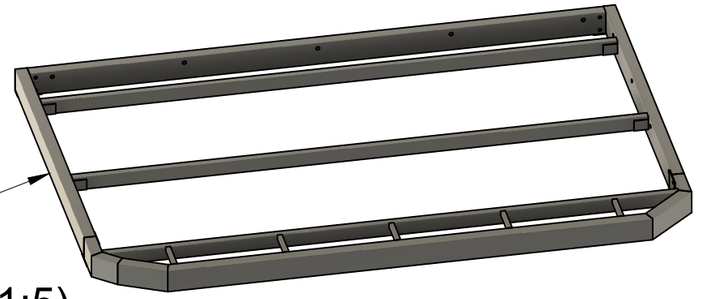


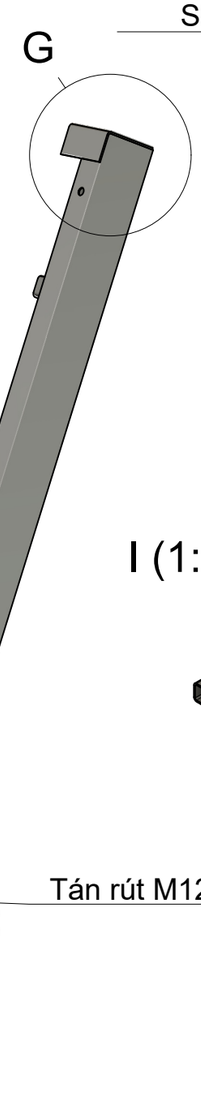


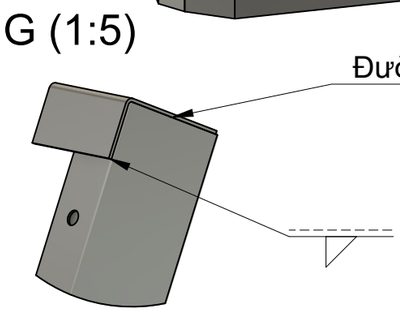

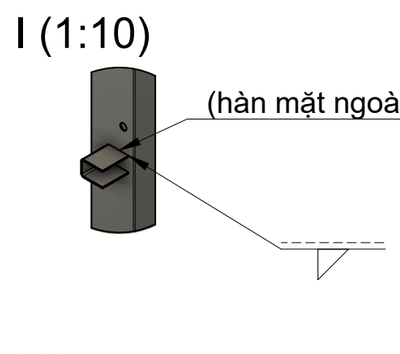


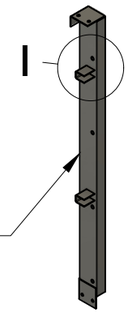


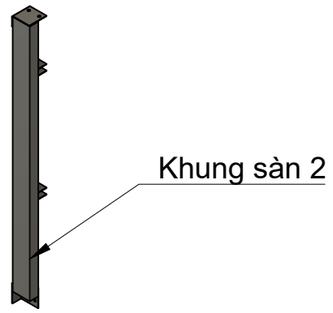


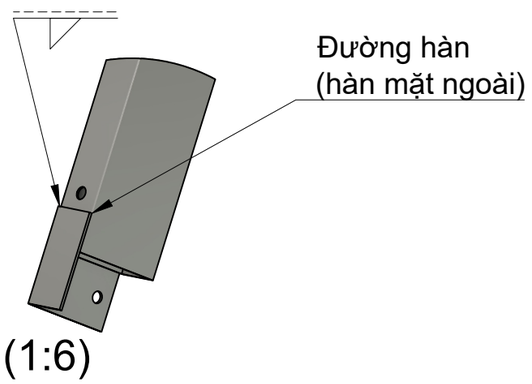



Title	Sheet
Khung sàn_2 SL :1	4/8

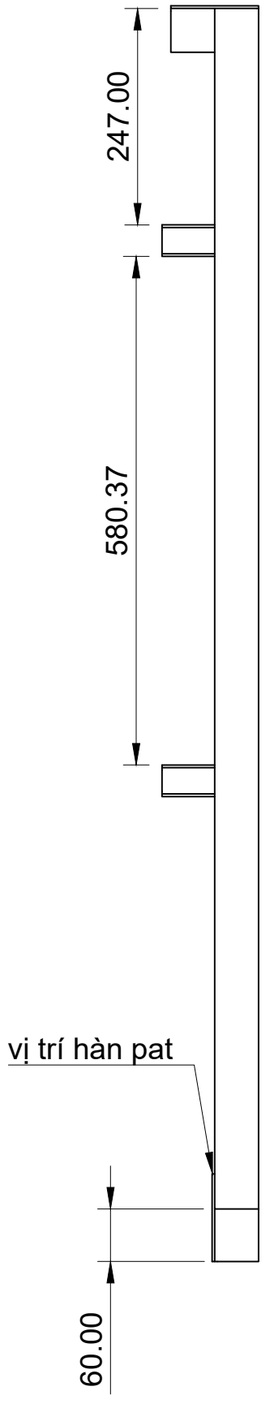

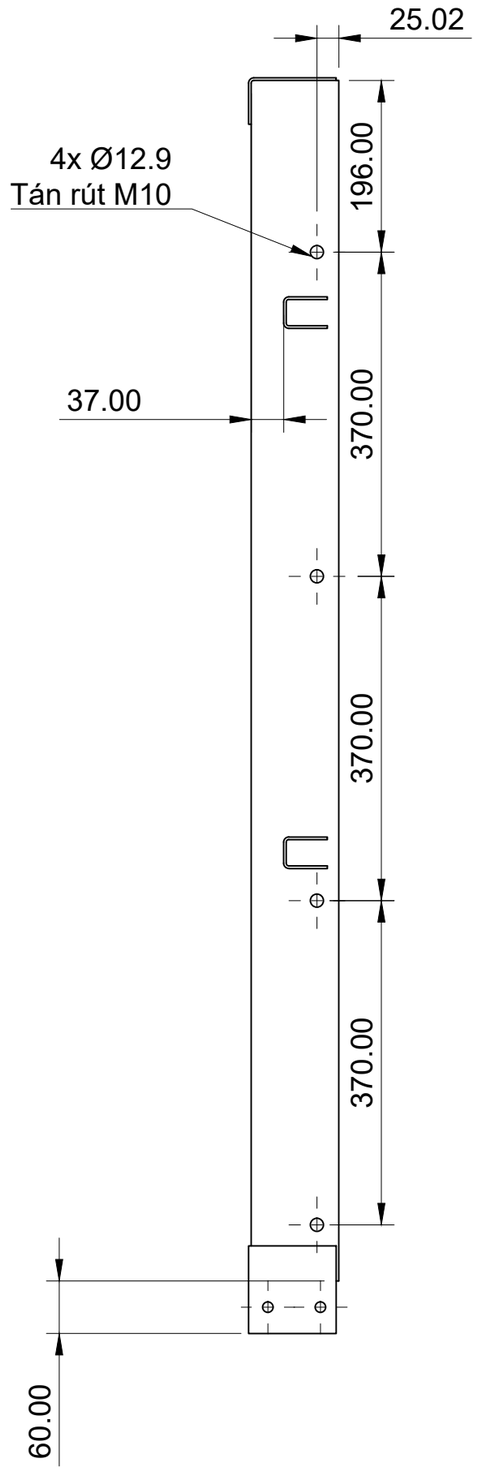


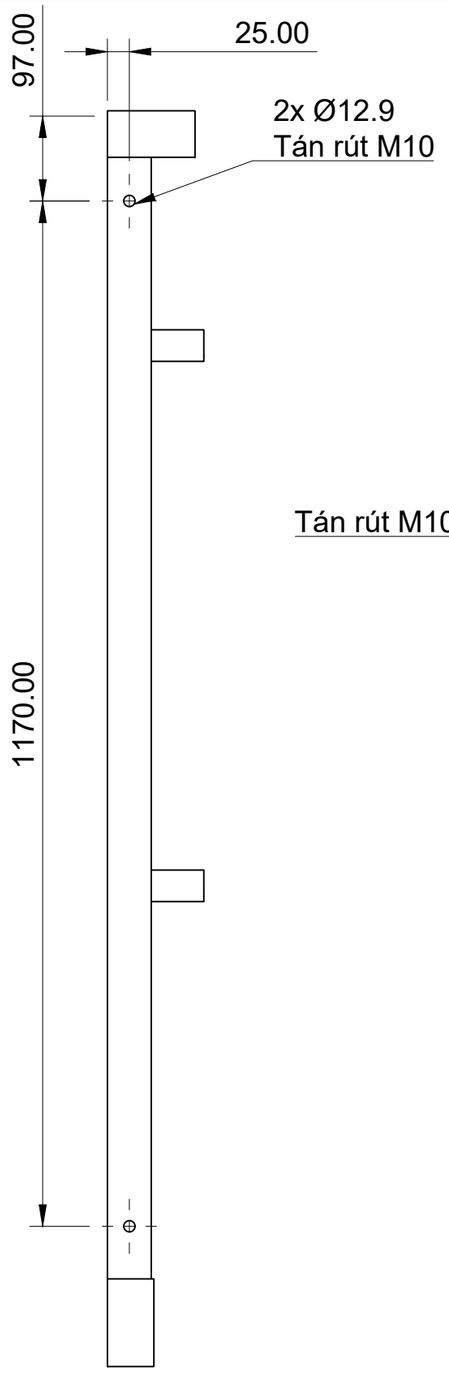


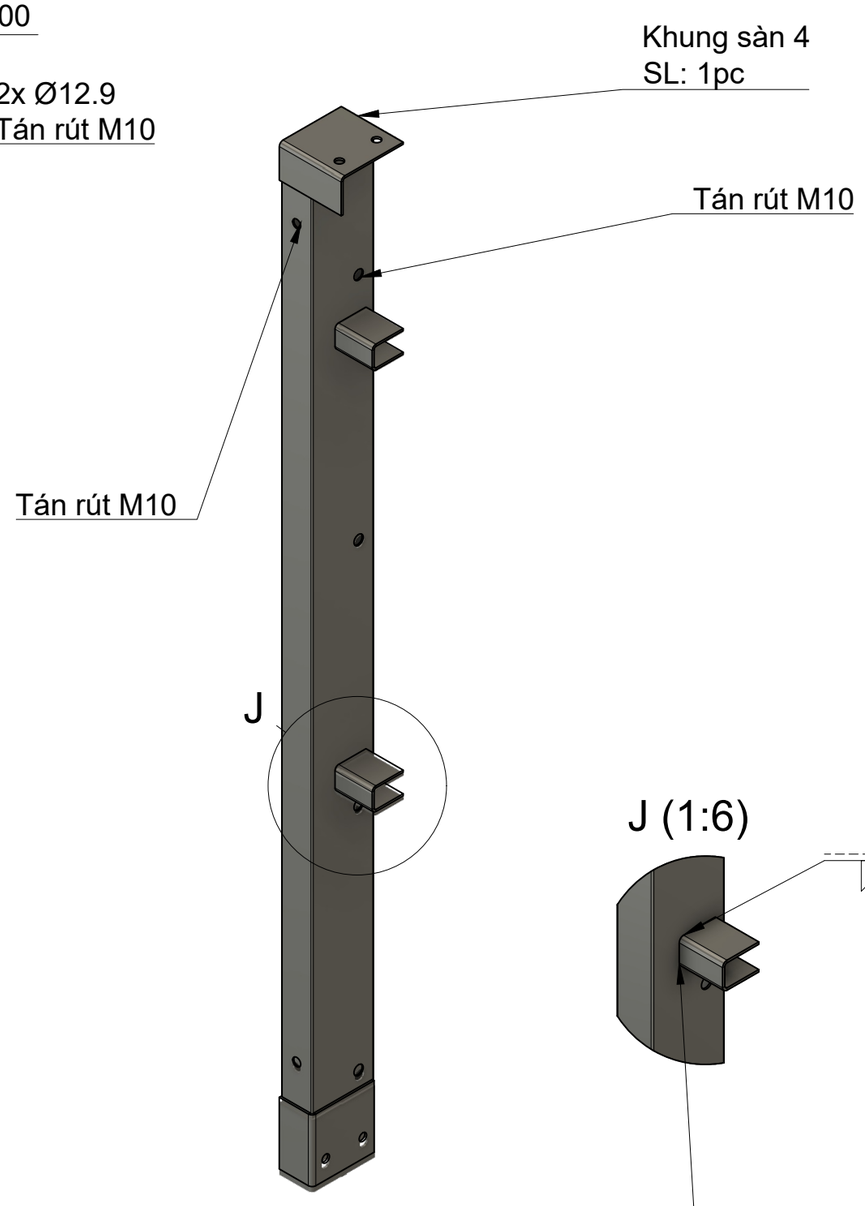


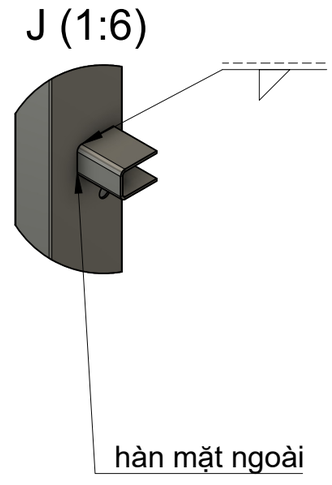



Title	Sheet
Khung sàn_4 SL: 1	5/8

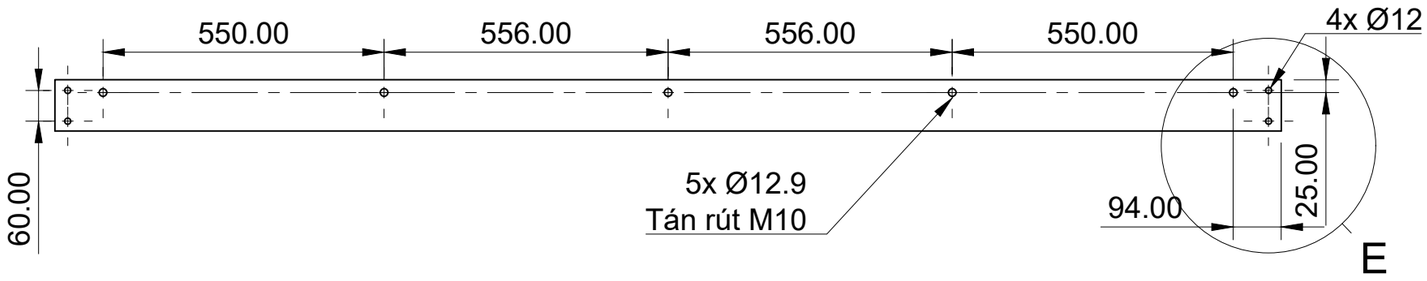


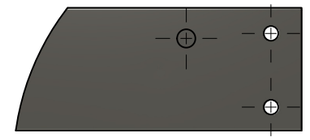


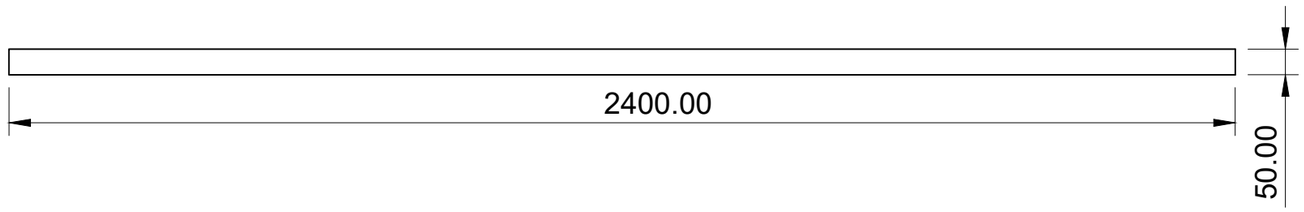

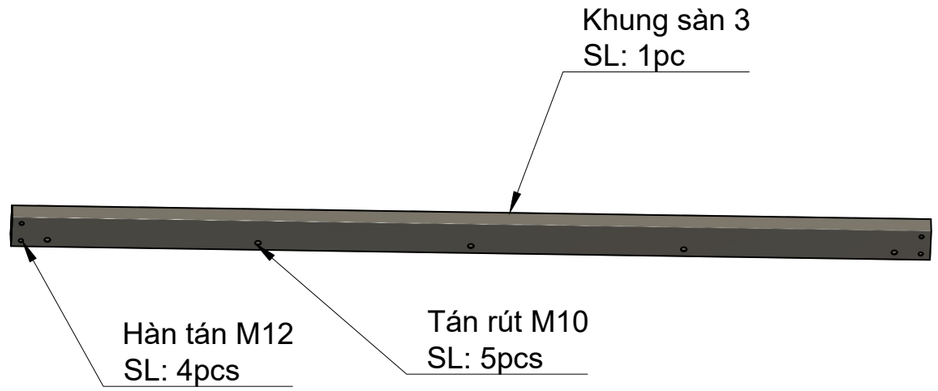


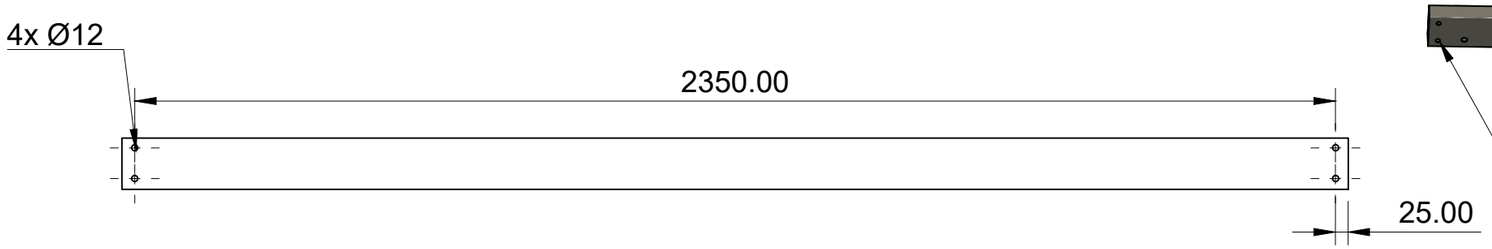

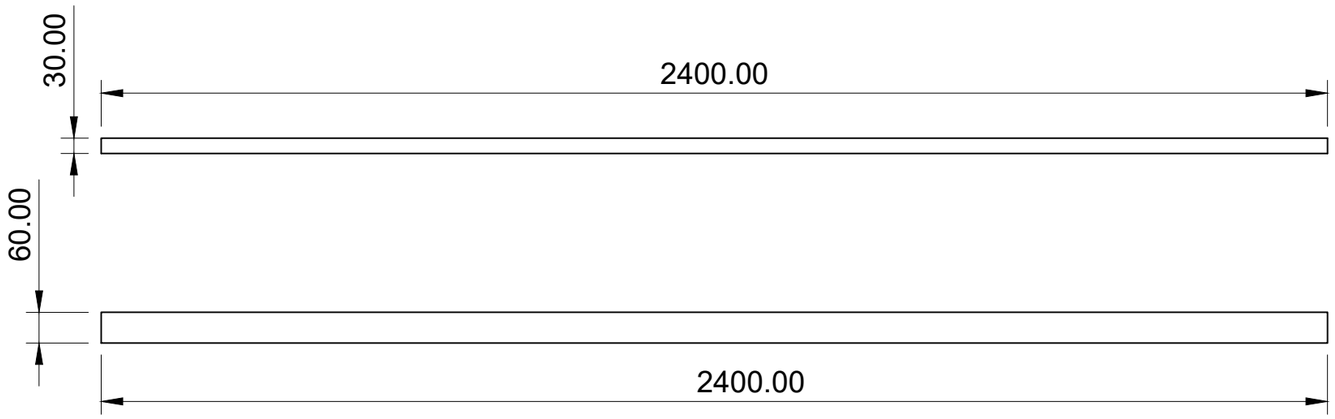


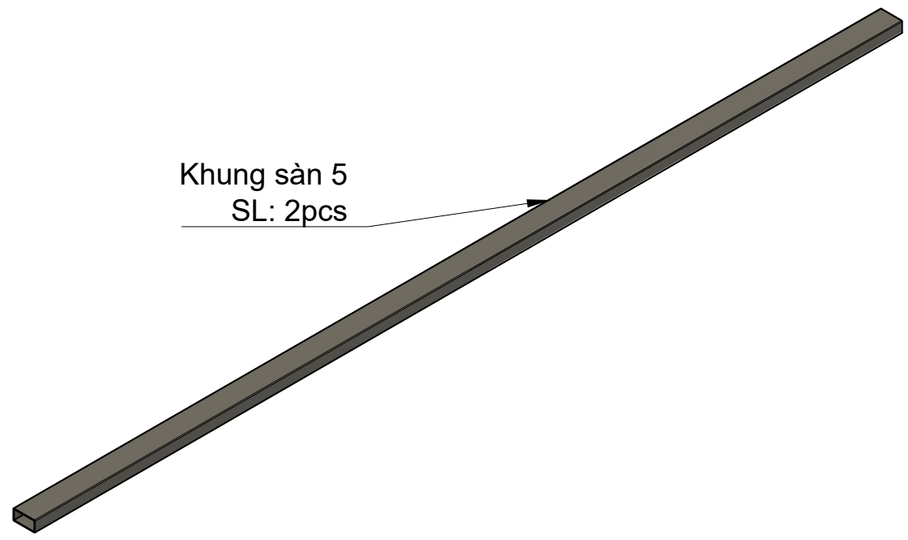



Title	Sheet
Khung sàn_3 & 5 SL: 1	6/8

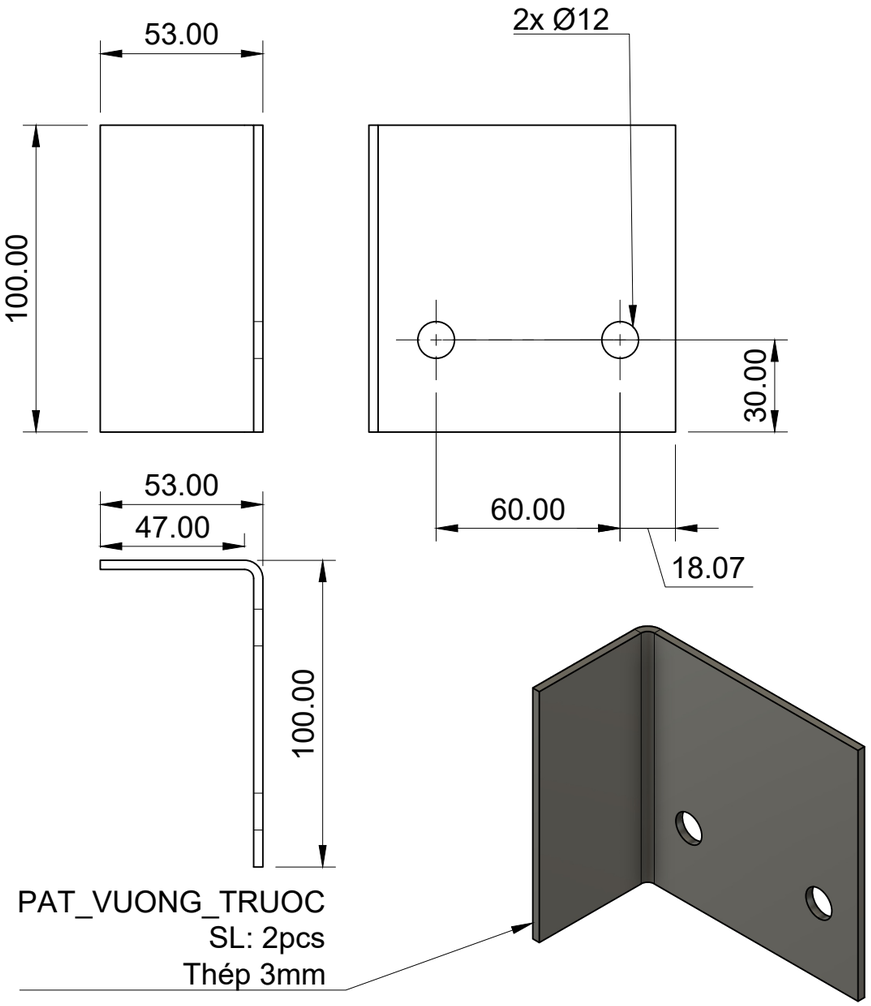

PAT_VUONG_TRUOC
SL: 2pcs
Thép 3mm

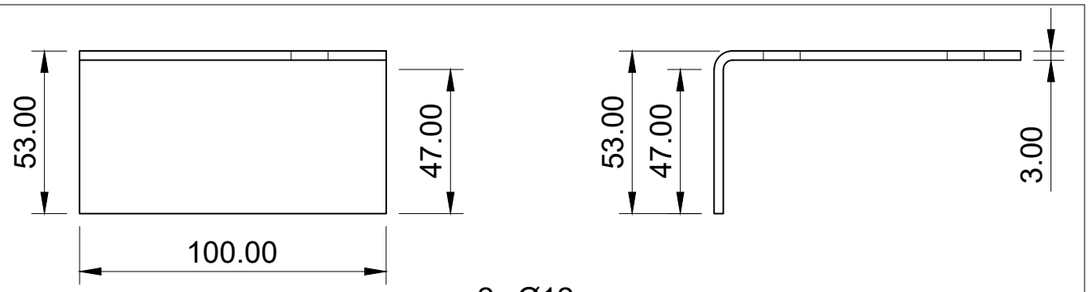


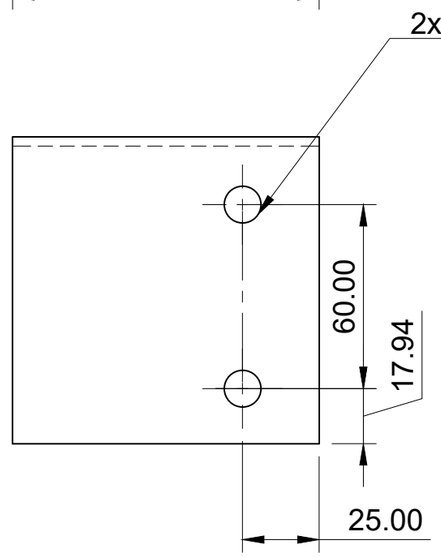


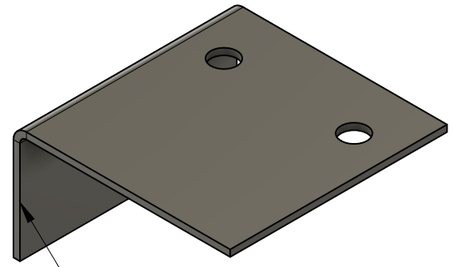


PAT_VUONG_SAU
SL: 2pcs
Thép 3mm


A (1:10)

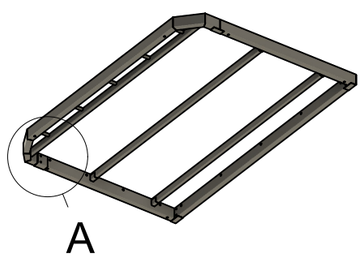

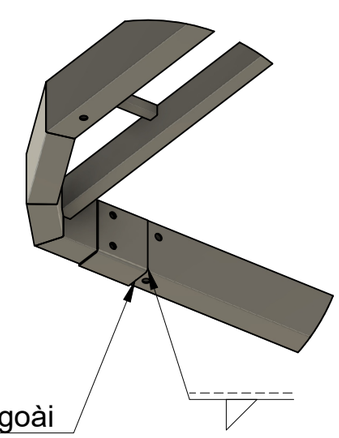



C (1:10)

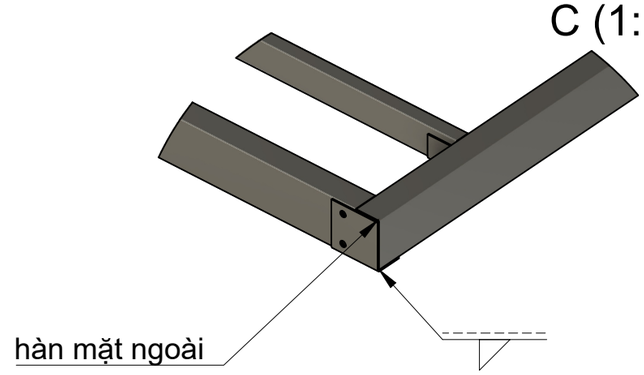


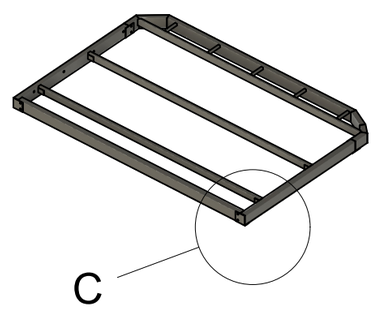



Title	Sheet
Pat_L	7/8

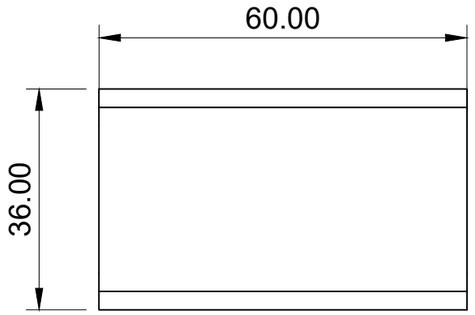


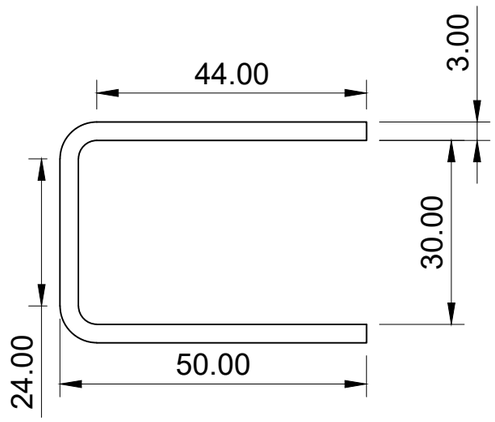

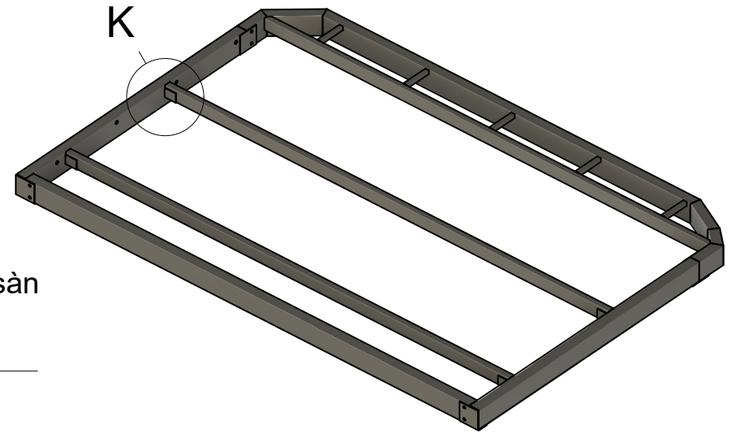


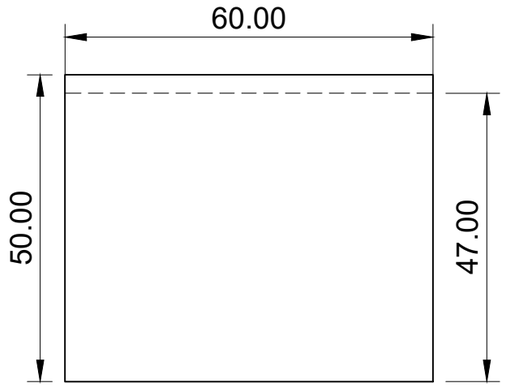

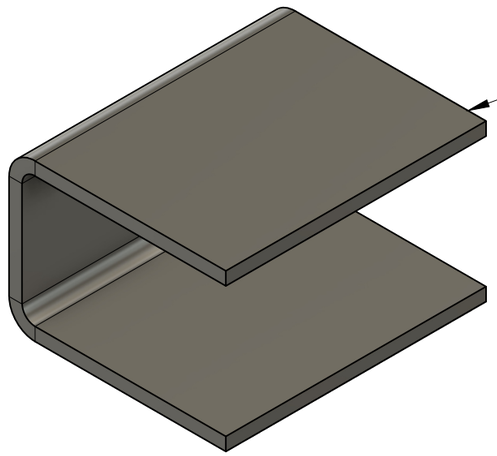


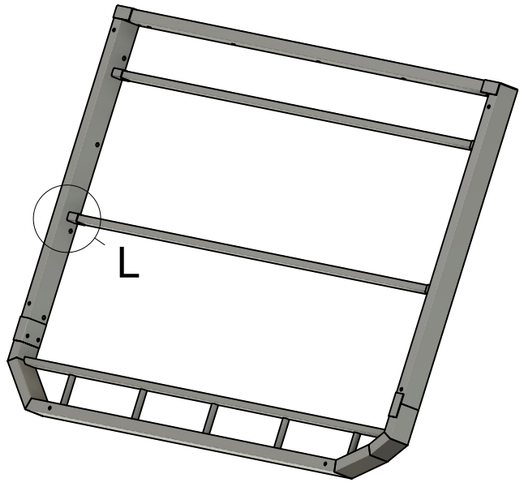


K (1:8)

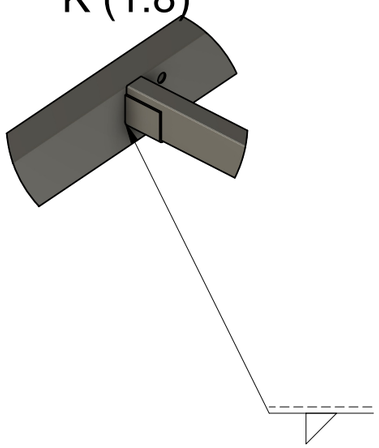



L (1:8)

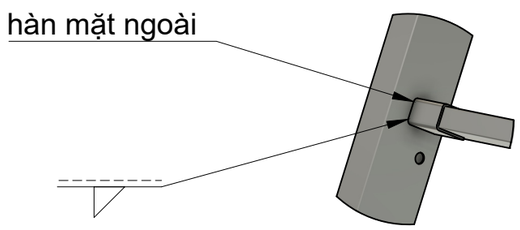



Title	Sheet
Pat_U SL: 4	8/8

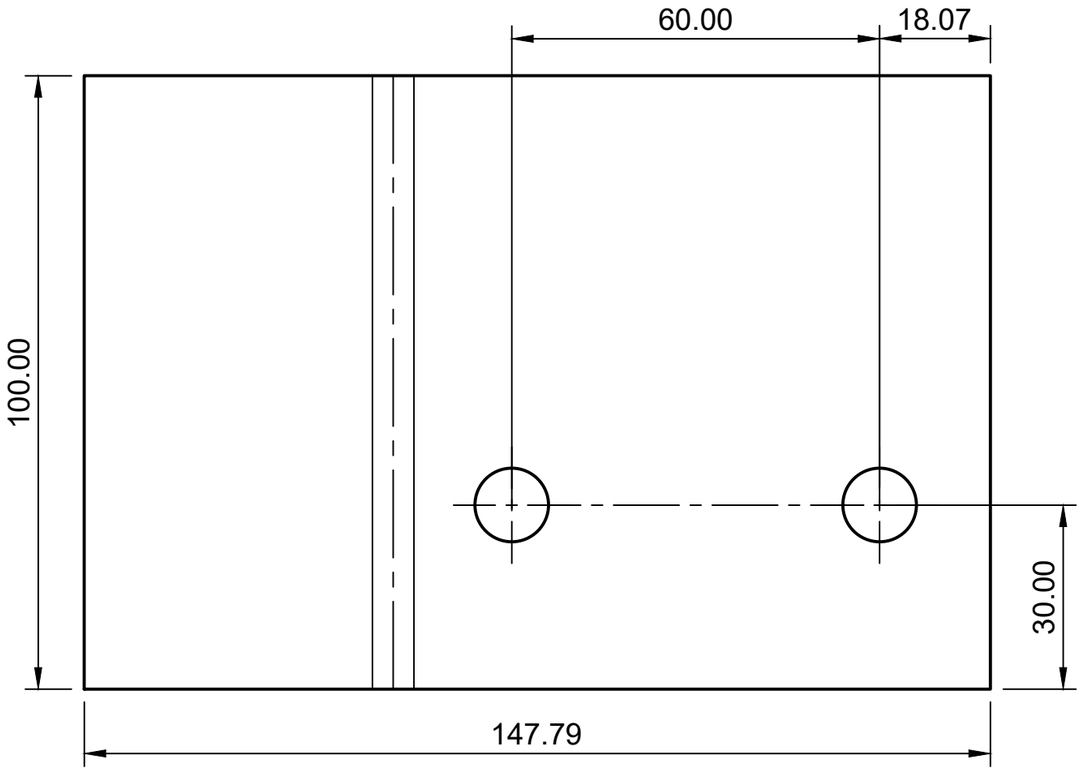


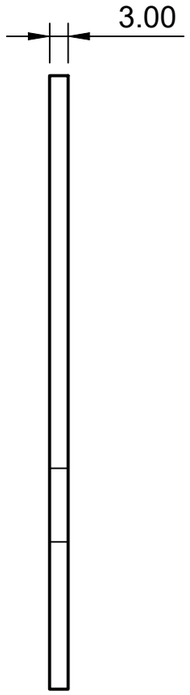

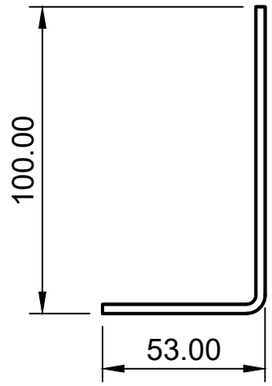


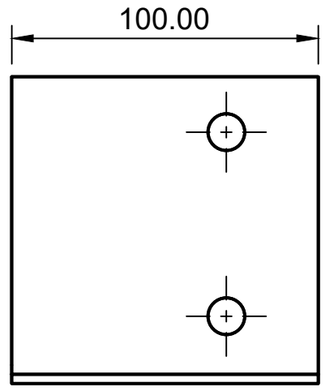

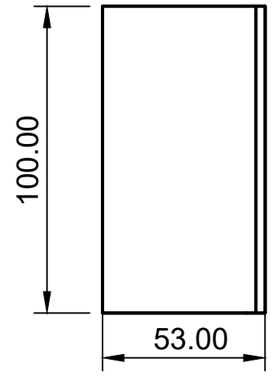

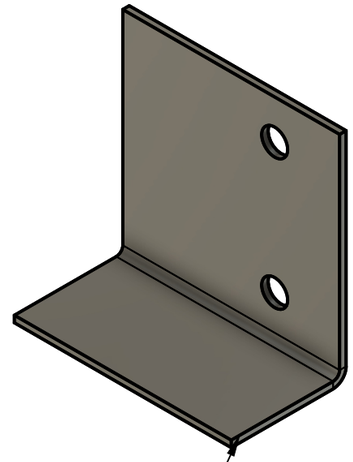



Pat_goctruoc_khungsan
Thép 3mm
SL: 2pcs

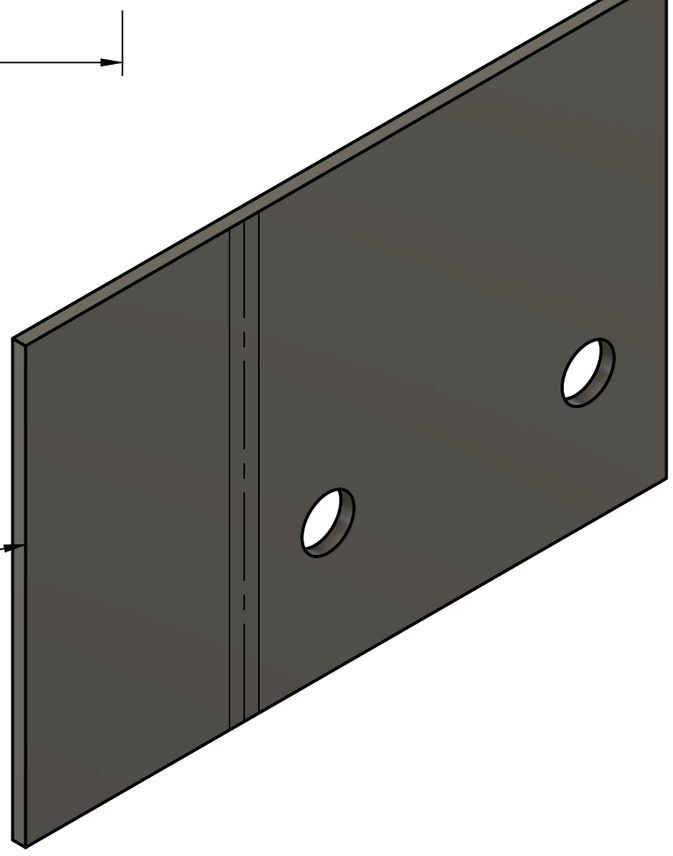


Pat_goctruoc_khungsan
Thép 3mm
SL: 2pcs
(Thép 3mm trải)


Pat_L_goc_truoc SL: 2	1/1

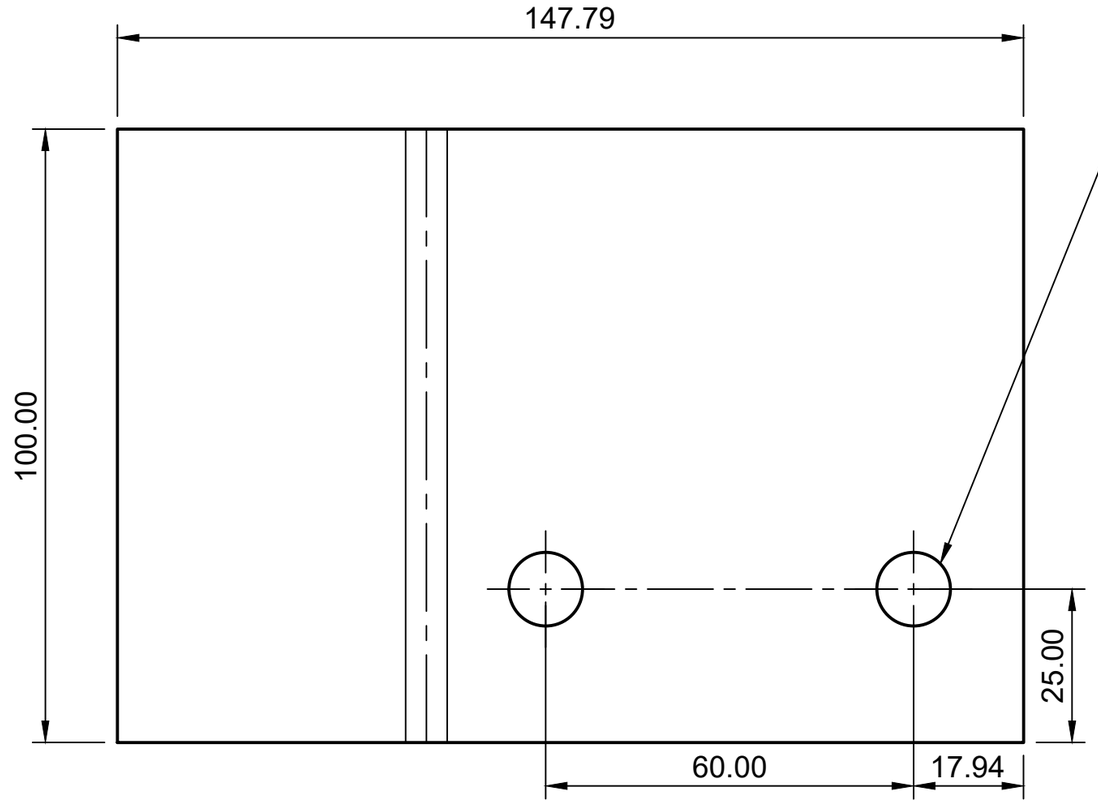

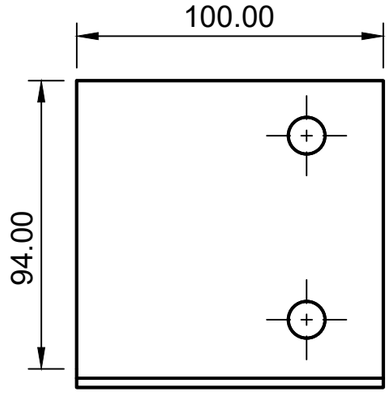


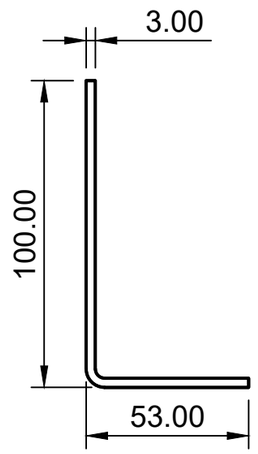



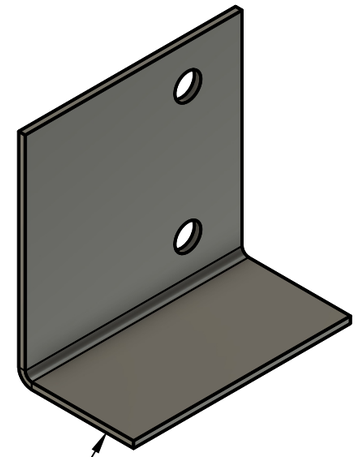



Pat_gocsau_khungsan
Thép 3mm
SL: 2pcs

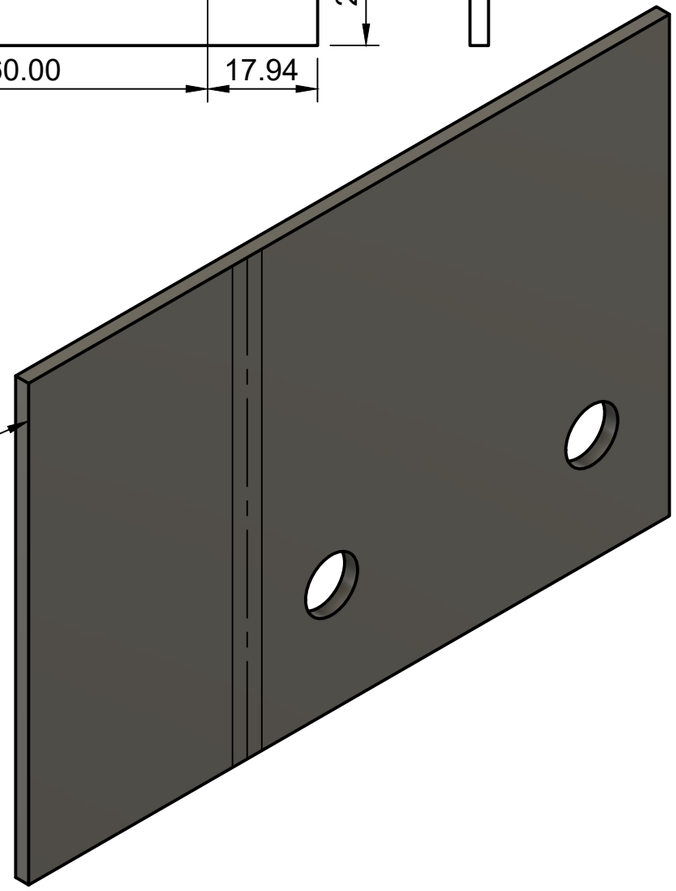



Pat_gocsau_khungsan
Thép 3mm
SL: 2pcs
Trải phẳng

Pat_L_goc_sau SL: 2	1/1

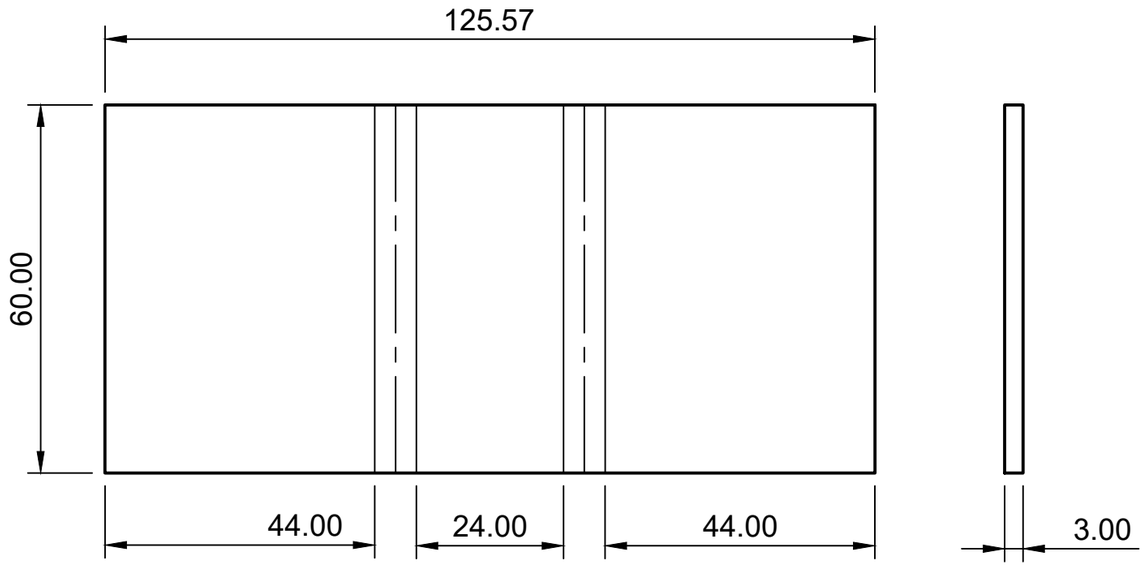

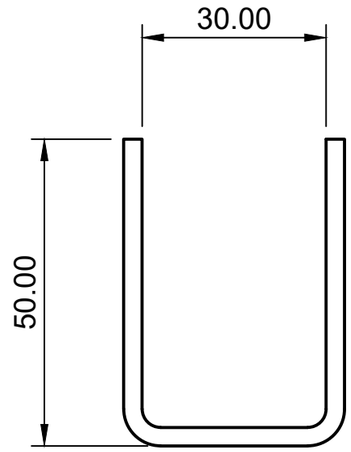


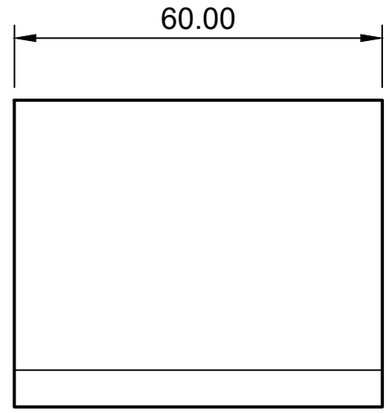

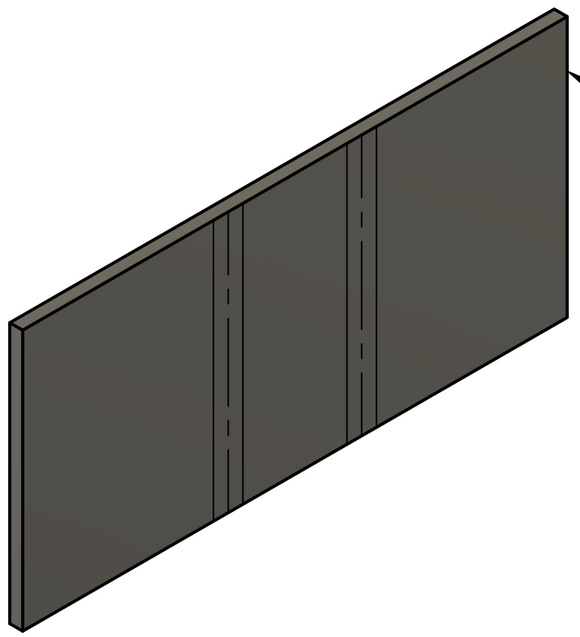


PAT_U_KHUNG SAN
THÉP 3MM TRẢI


PAT_U_KHUNG SAN
THÉP 3MM
SL: 4PCS

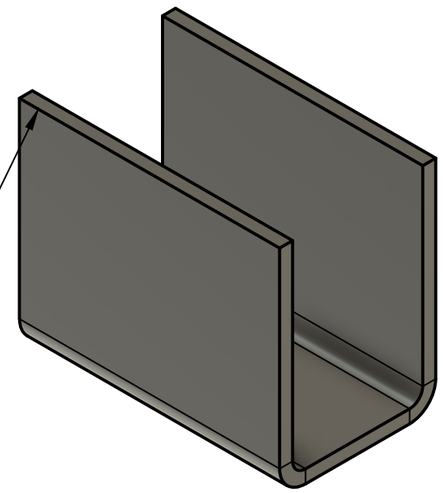



PAT_U SL: 4	1/1

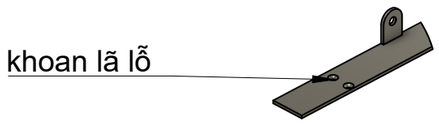


B (1:7)

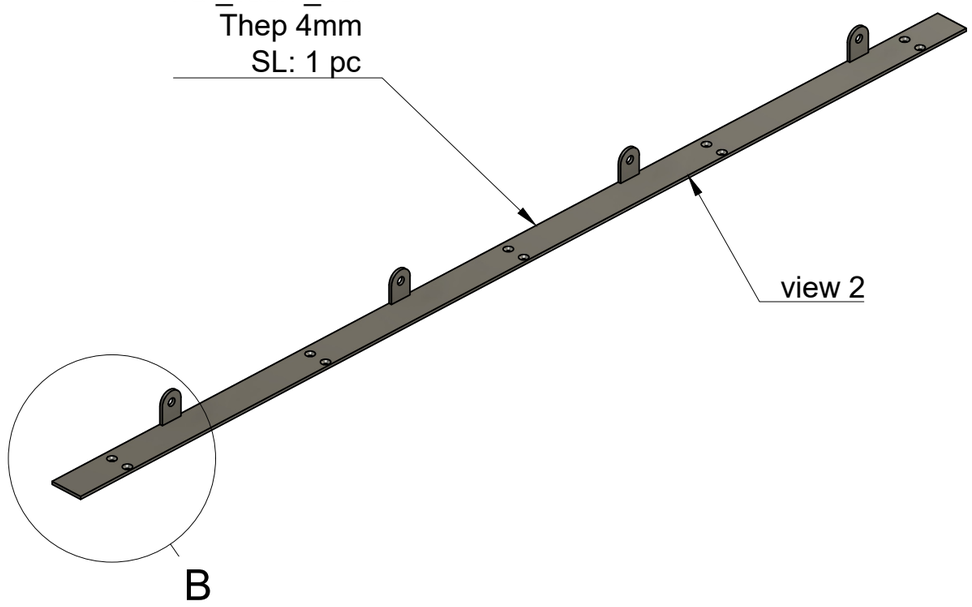


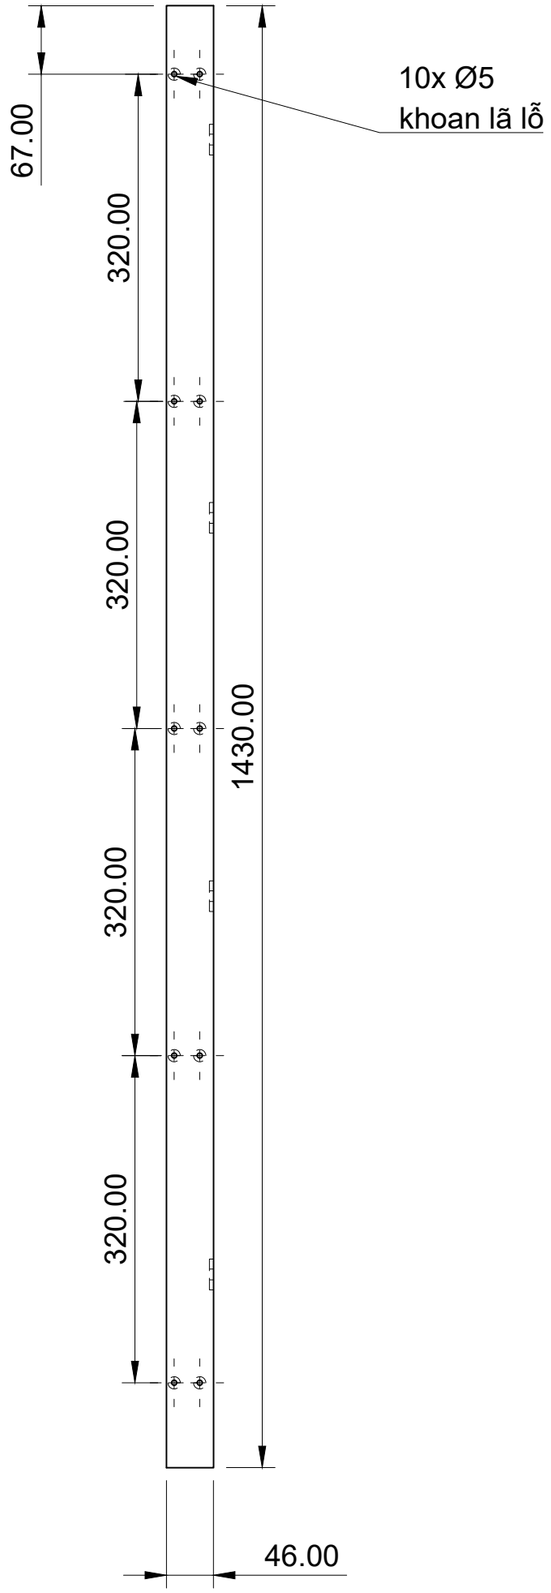

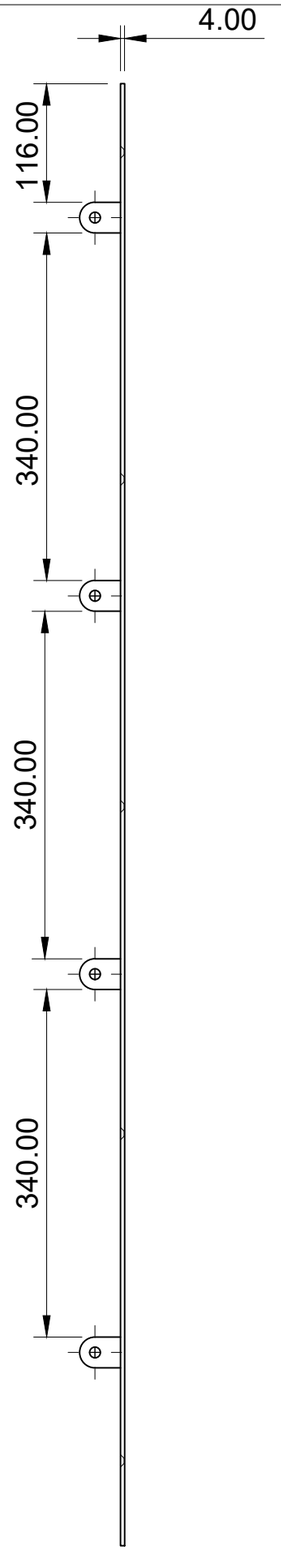



Title	Sheet
Pat_vach_trai SL: 1	1/2

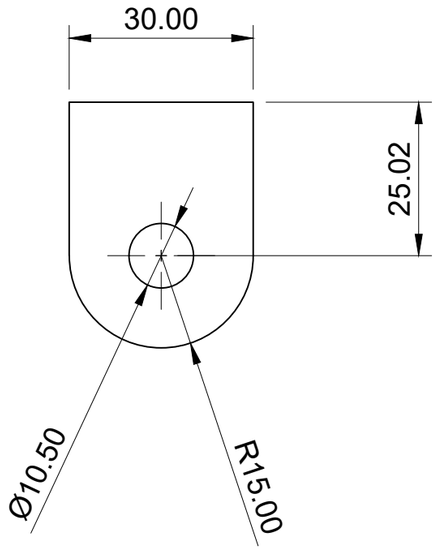

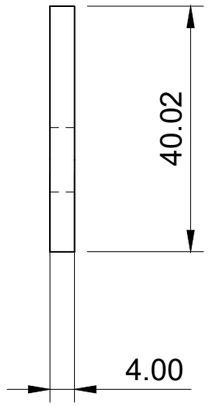



A (1:2)

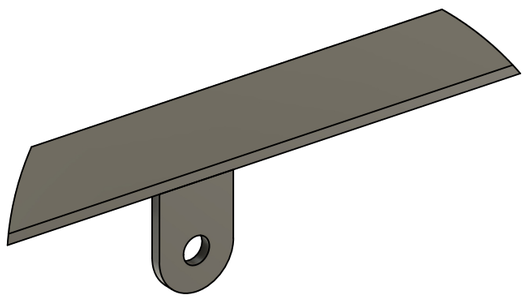

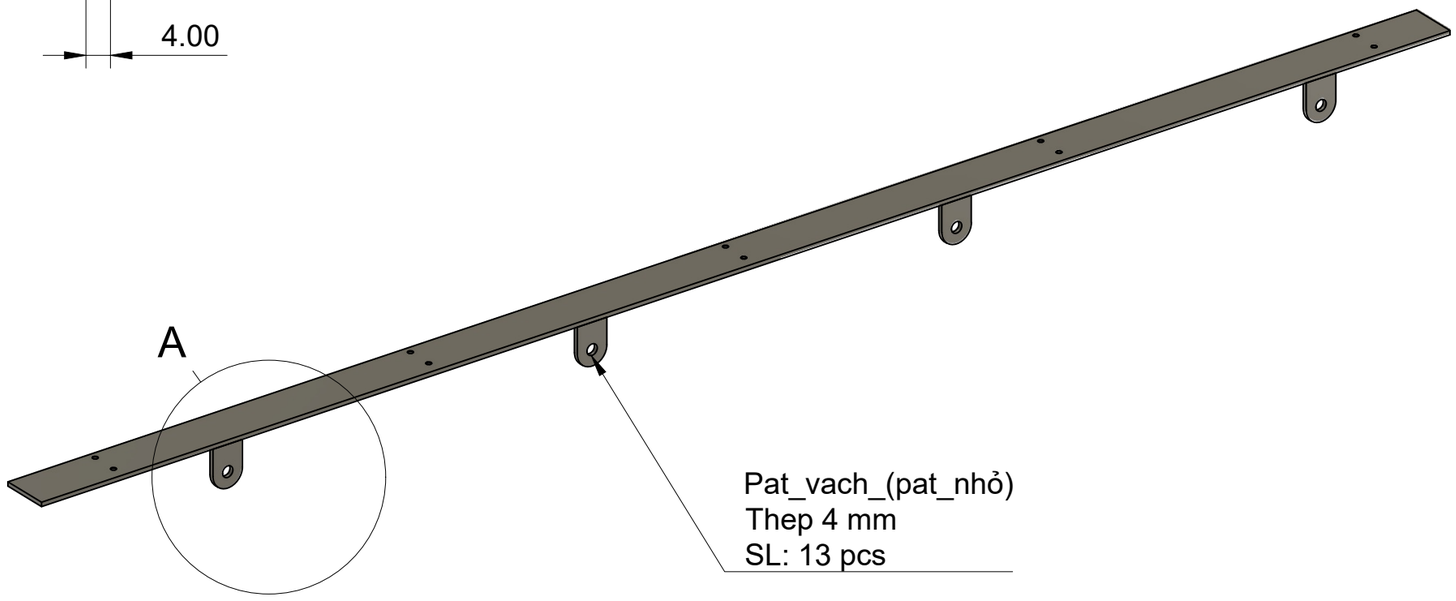


Title	Sheet
Pat_nho (dung chung) SL: 13	2/2

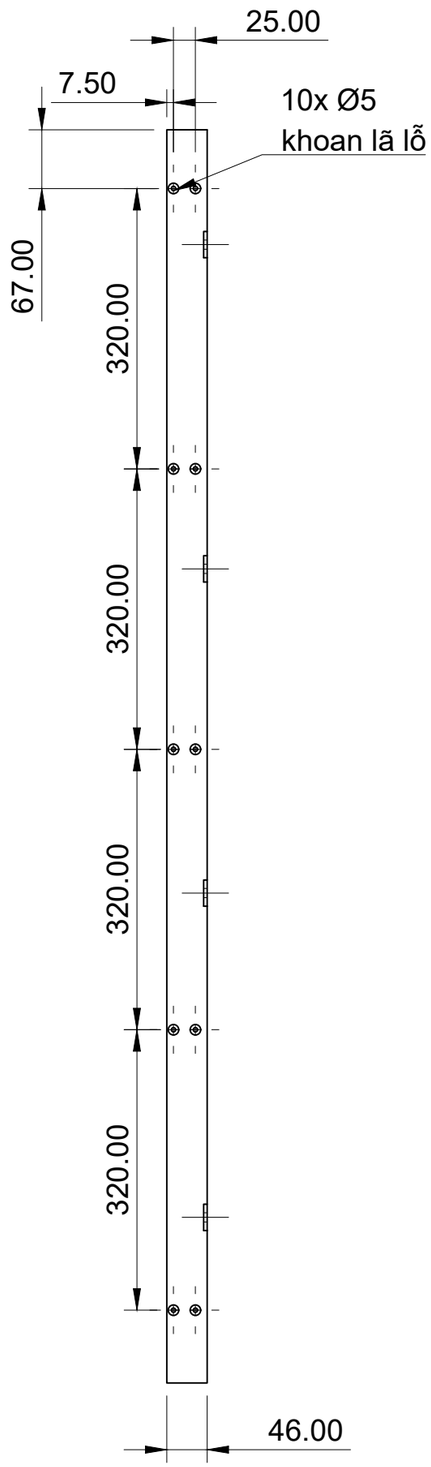

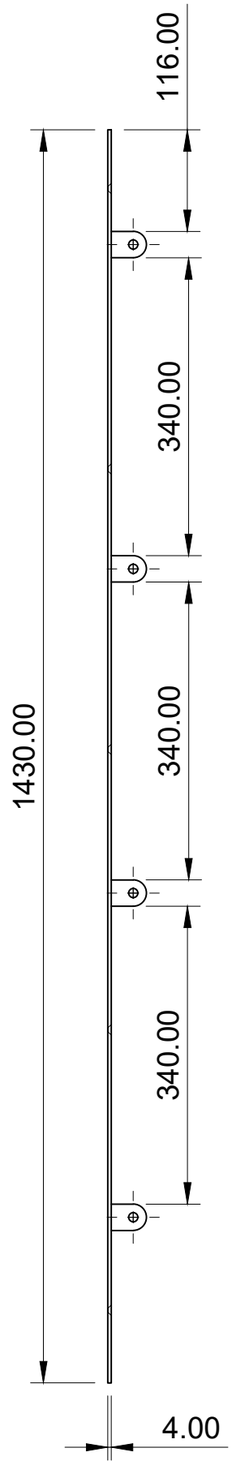


A (1:5)

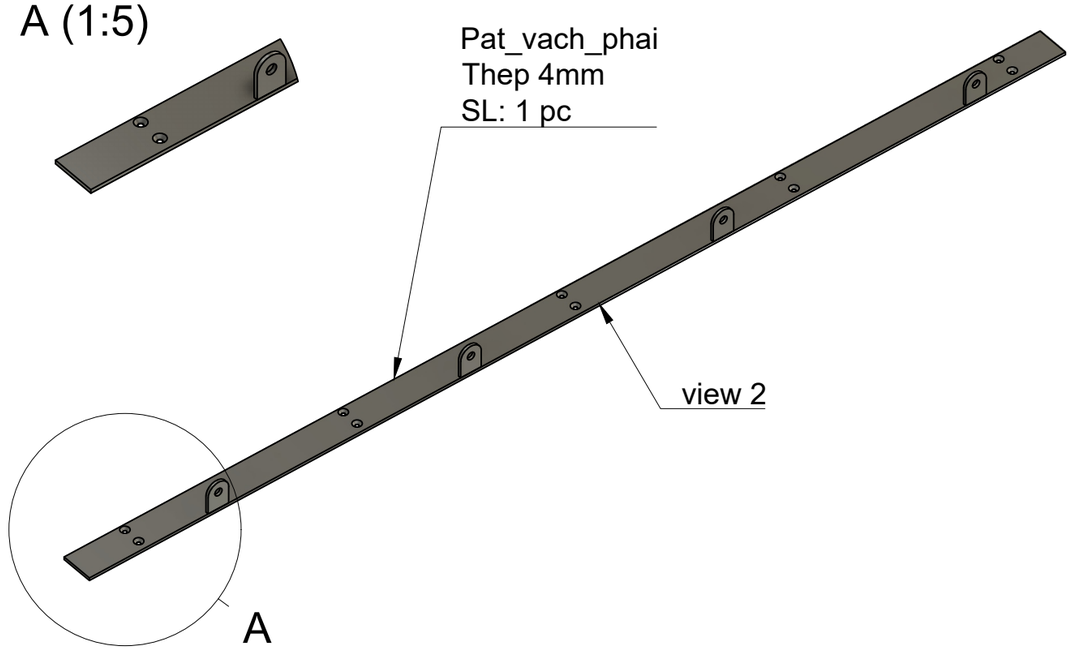



Title	Sheet
Pat_vach_phai SL: 1	1/1

A (1:5)

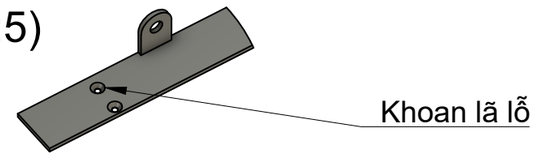


Khoan lã lỗ

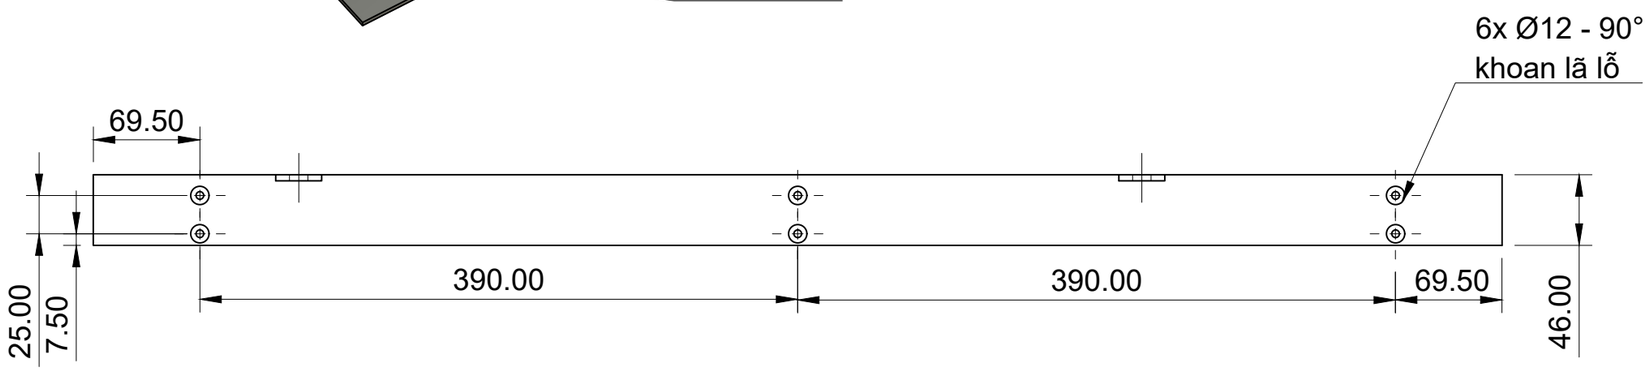


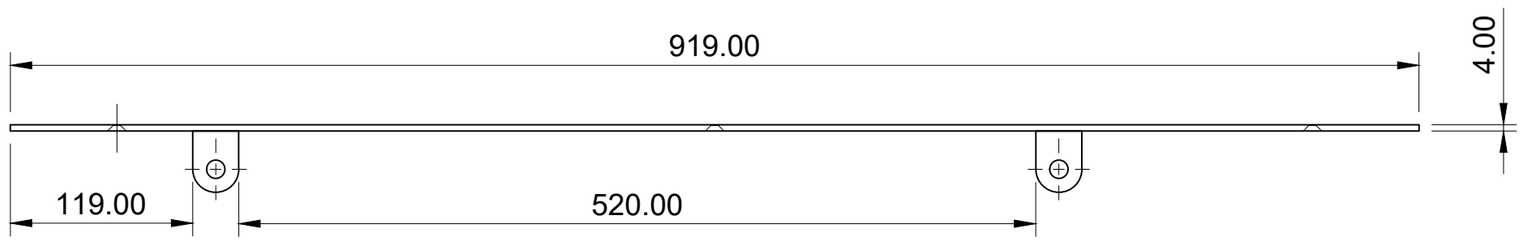


Pat_sau_vach_trai
Thep 3mm
SL: 1 pc

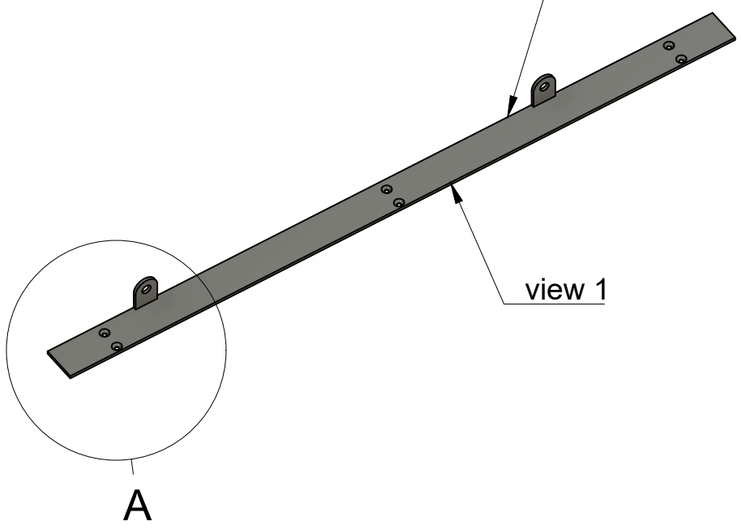


Title	Sheet
Pat_sau_vach_trai SL: 1	1/1

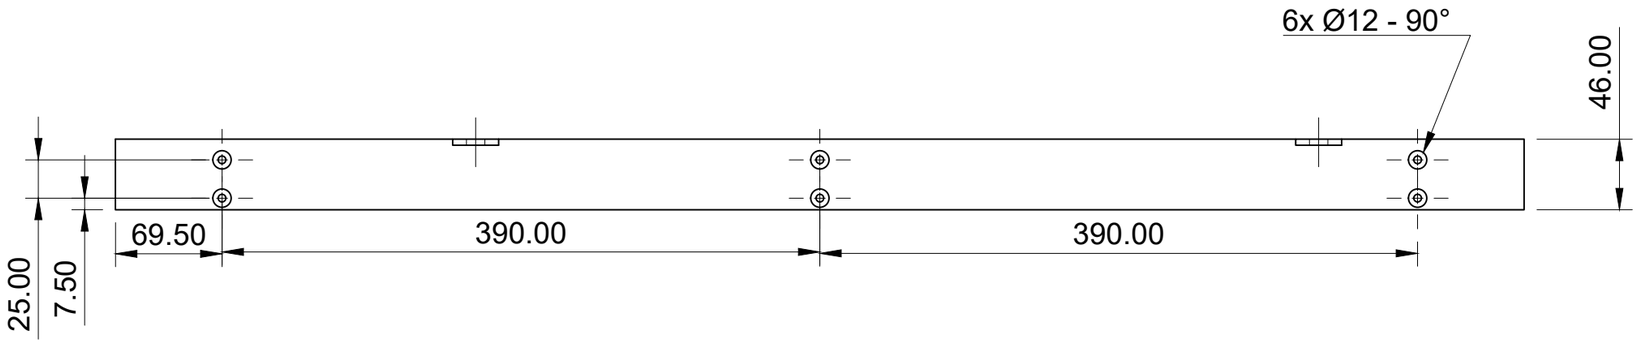

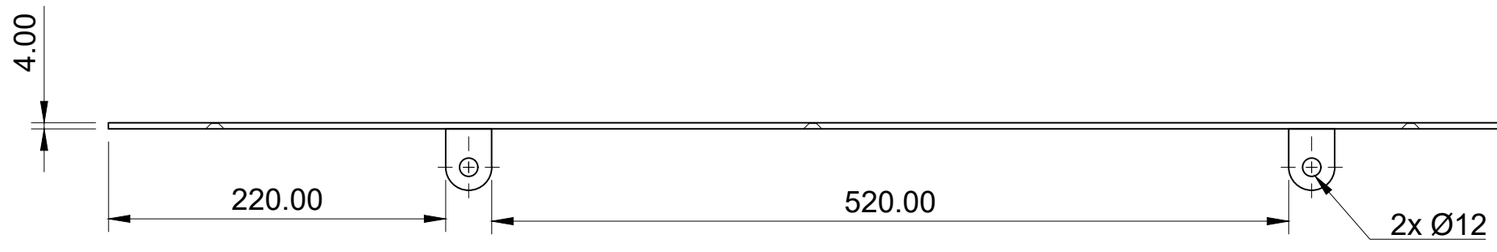


Pat_sau_vach_phai
Thep 4mm
SL: 1 pc

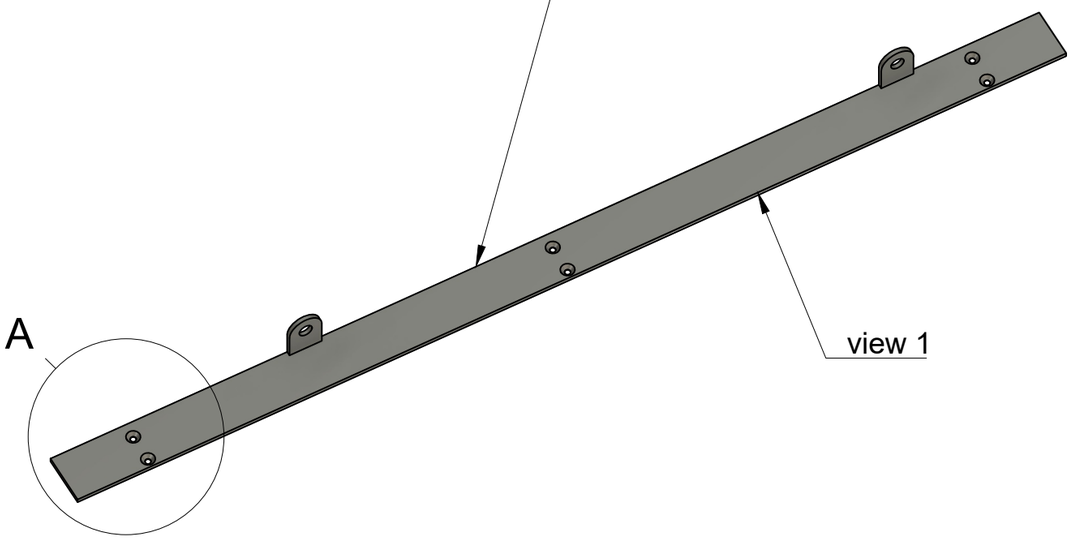



khoan lã lỗ

A (1:3)

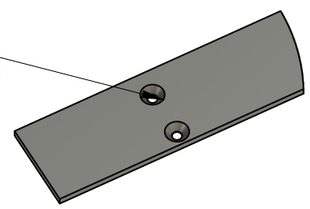


Title	Sheet
Pat_sau_vach_phai SL: 1	1/1

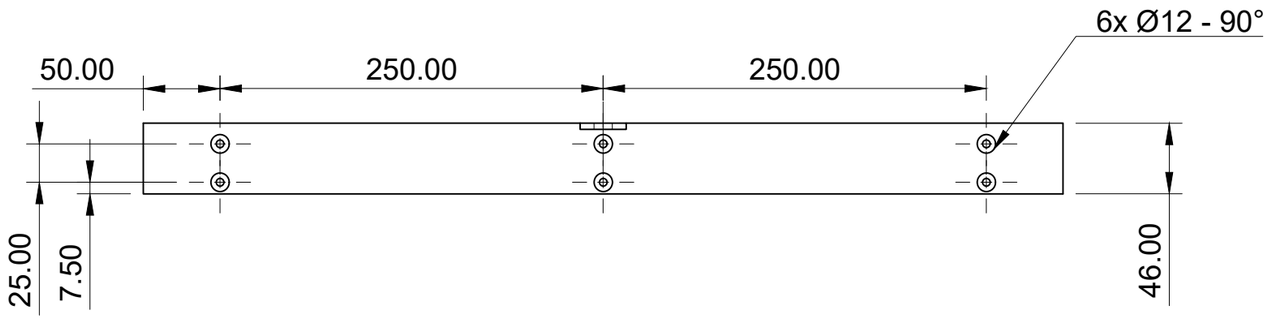

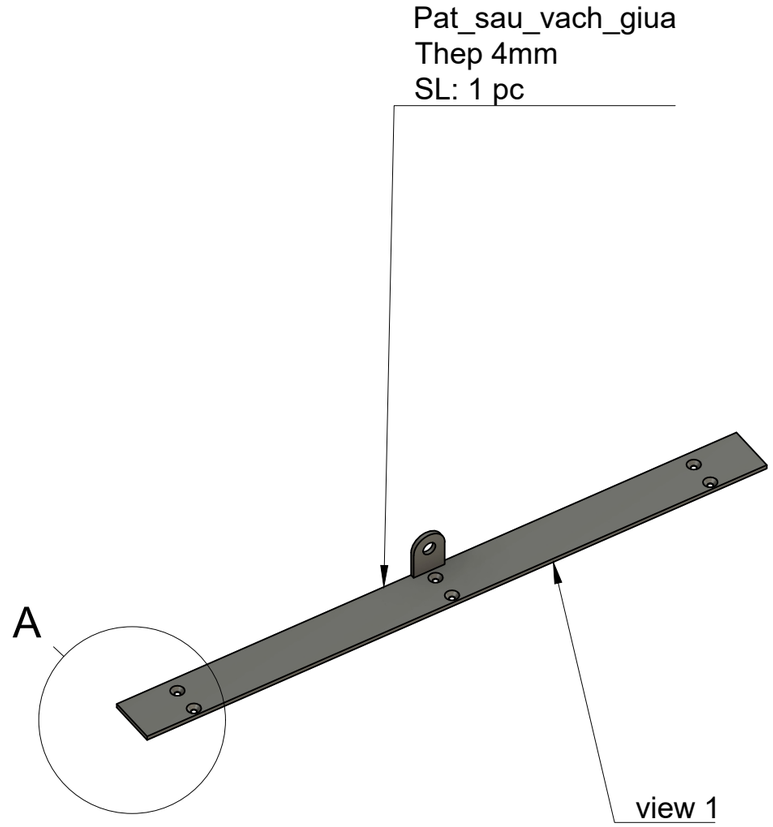

A (1:2)

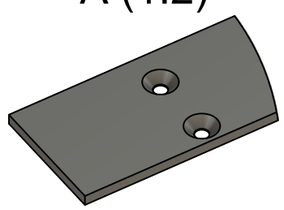

Title	Sheet
Pat_sau_vach_giua SL: 1	1/1