




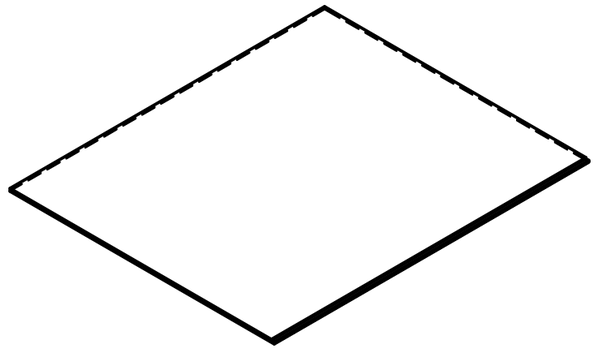

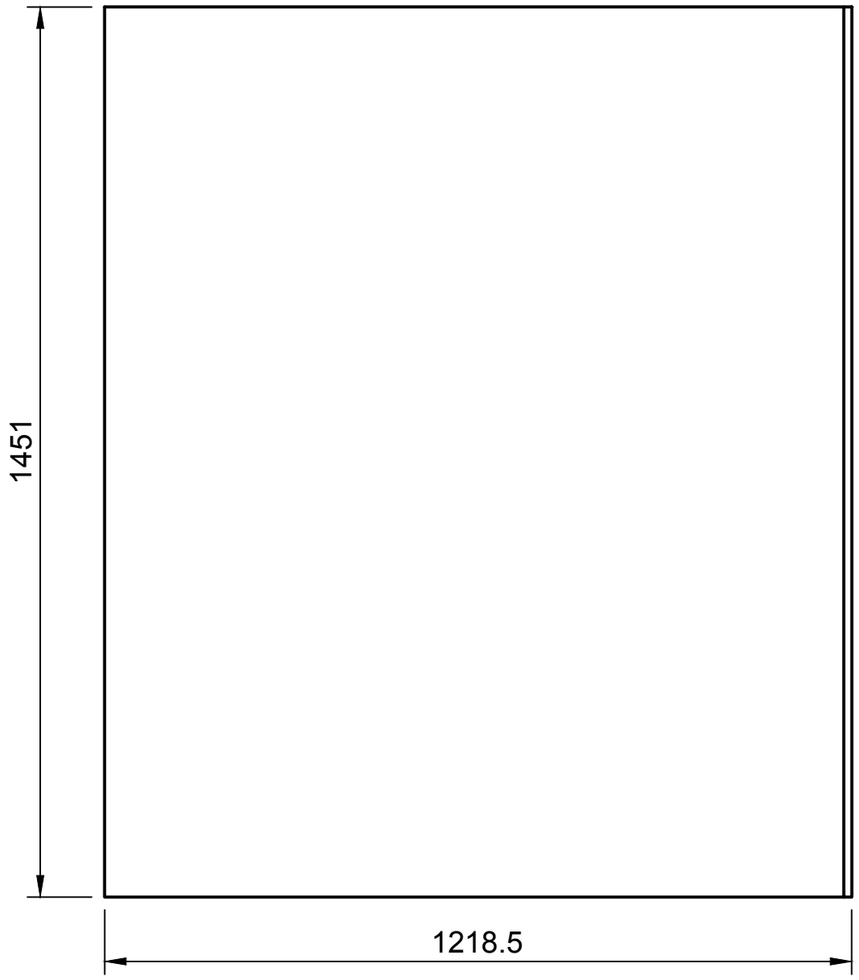

110401 BASE - FLOOR PANEL ASSY - F1 / Tấm sàn F1 (cụm dán)
Drawing 110401_P01_BASE-FLOOR-PANEL-ASSY-F1_DWG Rev P01 Status DRAFT (not for production) Sheet 1/1, A3 Scale 1:10 (iso 1:20)
UNITS: mm. Projection: ISO first angle (ISO 5456-2), symbol at right. Do not scale.
Material: bonded subassembly: F1 plywood with its foam mat bonded underneath at the factory (D-87); adhesive spec HOLD
Finish: none
Process: bond (spec HOLD)
Mass: see the parts list
Tolerances: Assembly: parts to their own drawings (the doubler 111601 to its DXF and parts-list row, the foam mat 111501 to its DXF, D-89); positions from skeleton P04 (110000_P01_BASE_CAD), hardware as the joints register (J-BASE-01, J-BASE-02).
Datums and axes: Pod coordinates (conventions §4), as built: floor panel F1 with its 3 mm foam mat bonded underneath at the factory (D-87), the mat under the lap too; ply Z 3 to 12, floor top Z 12 (skeleton floor_top). Adhesive HOLD.
Holes: No holes.
Sources: CAD 110000_P01_BASE_CAD and the part's own design; feature reasons in v2/02-Drawings/base/FEATURE-RATIONALE.md; status of every number in base_build.py.
Made by the BASE Engineer (AI agent), v2/02-Drawings/base/base_drawings.py, 2026-11-01.
PARTS LIST (from 110000_P01_BASE_BOM.csv):
111401 BASE - FLOOR PANEL - F1 x 1 pcs
111501 BASE - FLOOR FOAM - F1 - CLOSED-CELL 3 MM x 1 pcs

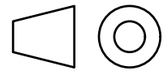

Dept.	Technical reference	Created by 31/10/26	Approved by
		Document type	Document status DRAFT
		Title BASE - FLOOR PANEL ASSY - F1	DWG No. 110401
			Rev. P01 / Date of issue / Sheet 1/1